

Эскизный проект жилого дома



Ведомость чертежей ЭП

Лист	Наименование	Примечание
1	Титульный лист	
2	Общие данные	
3	Экспликация помещений 1-го этажа	
4	План 1-го этажа	
5	План 2-го этажа	
6	План подвала. план на отметке +6,080	
7	Перспектива Вид 1	
8	Перспективный вид	
9	Перспектива Вид 2	
10	Фасад в осях 1-6	
11	Фасад в осях 6-1	
12	Фасад в осях Е-А'	
13	Фасад в осях А'-Е	
14	Кладочный план 1-го этажа	
15	Кладочный план 2-го этажа	
16	Клад. план подвала, на отметке +6,080	
17	Разрез 1-1	
18	Разрез 2-2	
19	План кровли	
20	Смета окон	
21	Смета дверей	

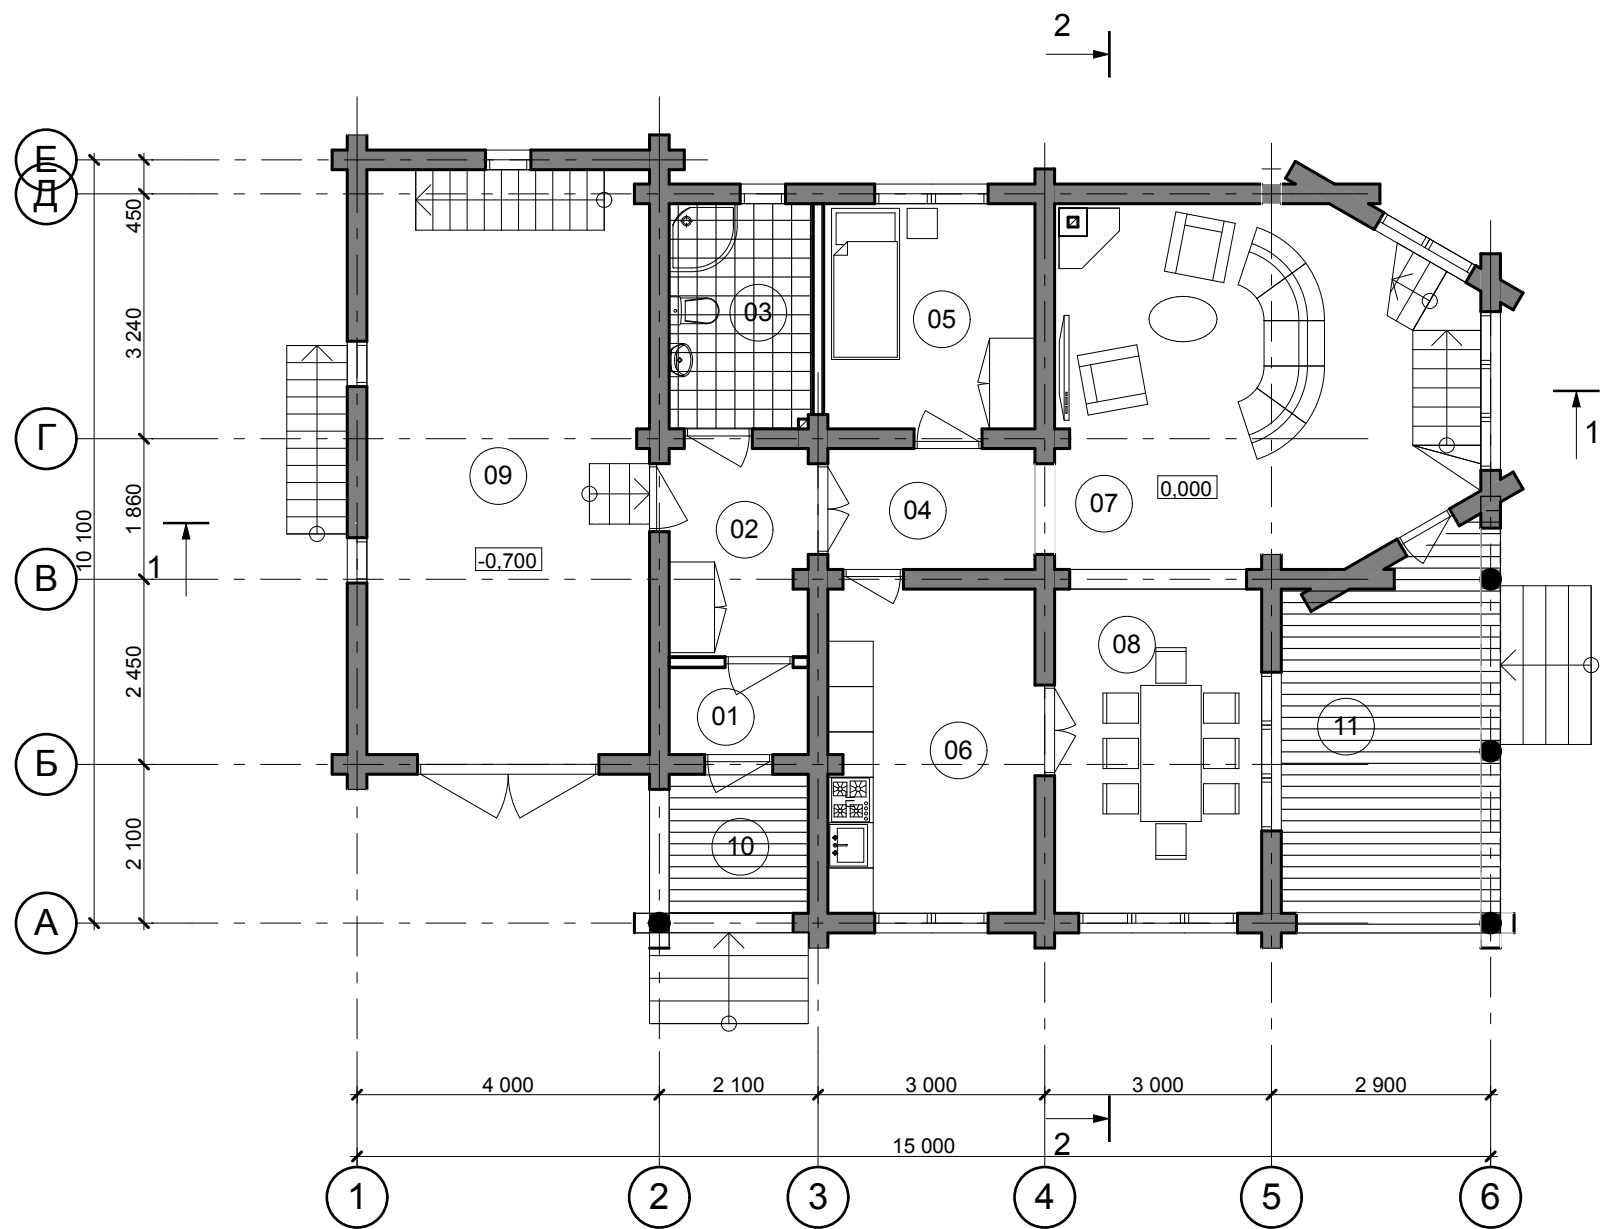
Технико-экономические показатели

п/п	Наименование	Количество, ед. измер.
1	Площадь участка	- м ²
2	Жилая площадь	78,6 м ²
3	Общая площадь	257,9 м ²
4	Площадь застройки	143,4 м ²
5	Строительный объем	1189,2 м ³
6	Этажность	3

Общие данные

Стадия	Лист	Листов
ЭП	2	21

Экспликация помещений 1-го этажа		
№	Наименование помещения	Площадь, кв.м.
01	Тамбур	2,1
02	Прихожая	5,0
03	С/у	5,6
04	Коридор	4,4
05	Спальня	8,3
06	Кухня	11,7
07	Гостиная	25,1
08	Столовая	11,8
09	Гараж	28,8
10	Крыльцо	3,4
11	Терраса	14,2
		120,4 м2



План 1-го этажа

Стадия	Лист	Листов
ЭП	4	21

Architectural floor plan of a building section. The plan shows four rooms labeled 01, 02, 03, and 04. Room 01 is at the top, followed by room 02, then room 03, and room 04 at the bottom. A staircase is located on the left side of the plan. The plan is bounded by grid lines Б, В, Г, Д, and Е on the left and 1, 2, and 3 on the bottom. Dimensions are provided for the overall section and individual rooms. A note indicates a level of -3.250.

Dimension	Value
Overall width (1 to 3)	6 100
Width of section 1 to 2	4 000
Width of section 2 to 3	2 100
Overall height (Б to Е)	8 000
Height of room 01	450
Height of rooms 02 and 03	3 240
Height of room 04	2 450
Height of section В to Г	1 860

Экспликация помещений на отм. 6,000		
№	Наименование помещения	Площадь, кв.м.
09	Игровая	30,8
		30,8 м2

№	Наименование помещения	Площадь, кв.м.
01	Погребок	8,7
02	Бойлерная	5,7
03	Топочная	6,0
04	Угольная	7,1
		27,5 м2

[illegible]

Стадия	Лист	Листов
ЭП	6	21



Перспектива Вид 1

Стадия	Лист	Листов
ЭП	7	21




Перспективный вид

Стадия	Лист	Листов
ЭП	8	21



Перспектива Вид 2

Стадия	Лист	Листов
ЭП	9	21

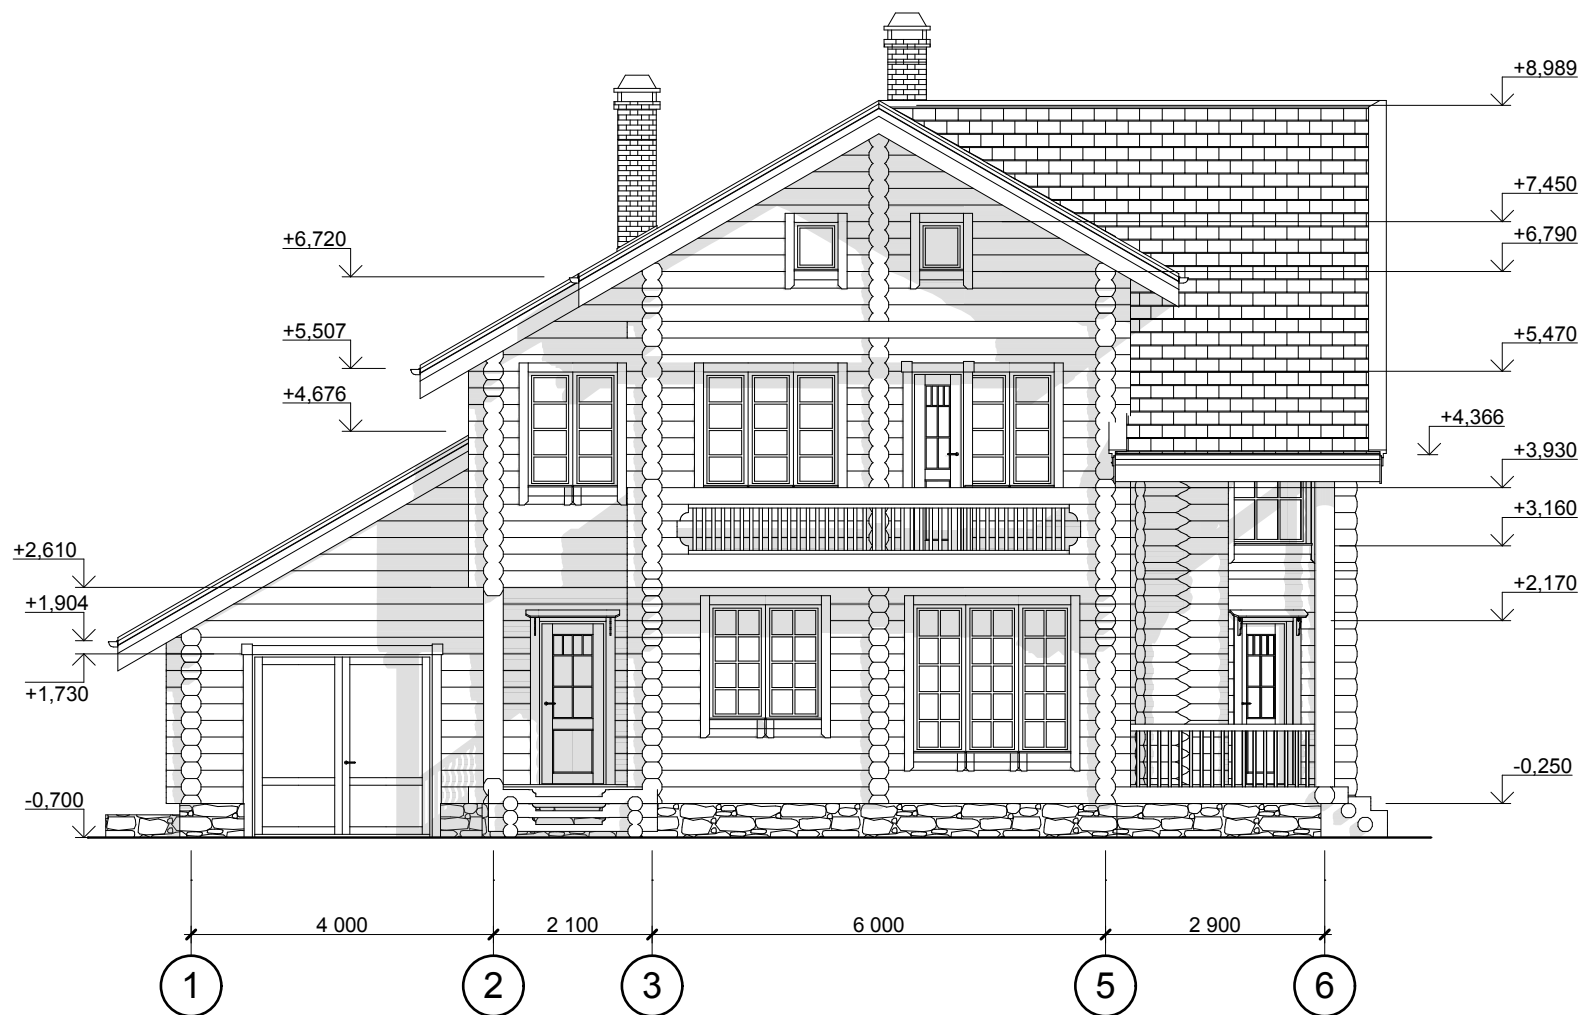


Фасад в осях 1-6

Стадия	Лист	Листов
ЭП	10	21




Фасад в осях 6-1

Стадия	Лист	Листов
ЭП	11	21

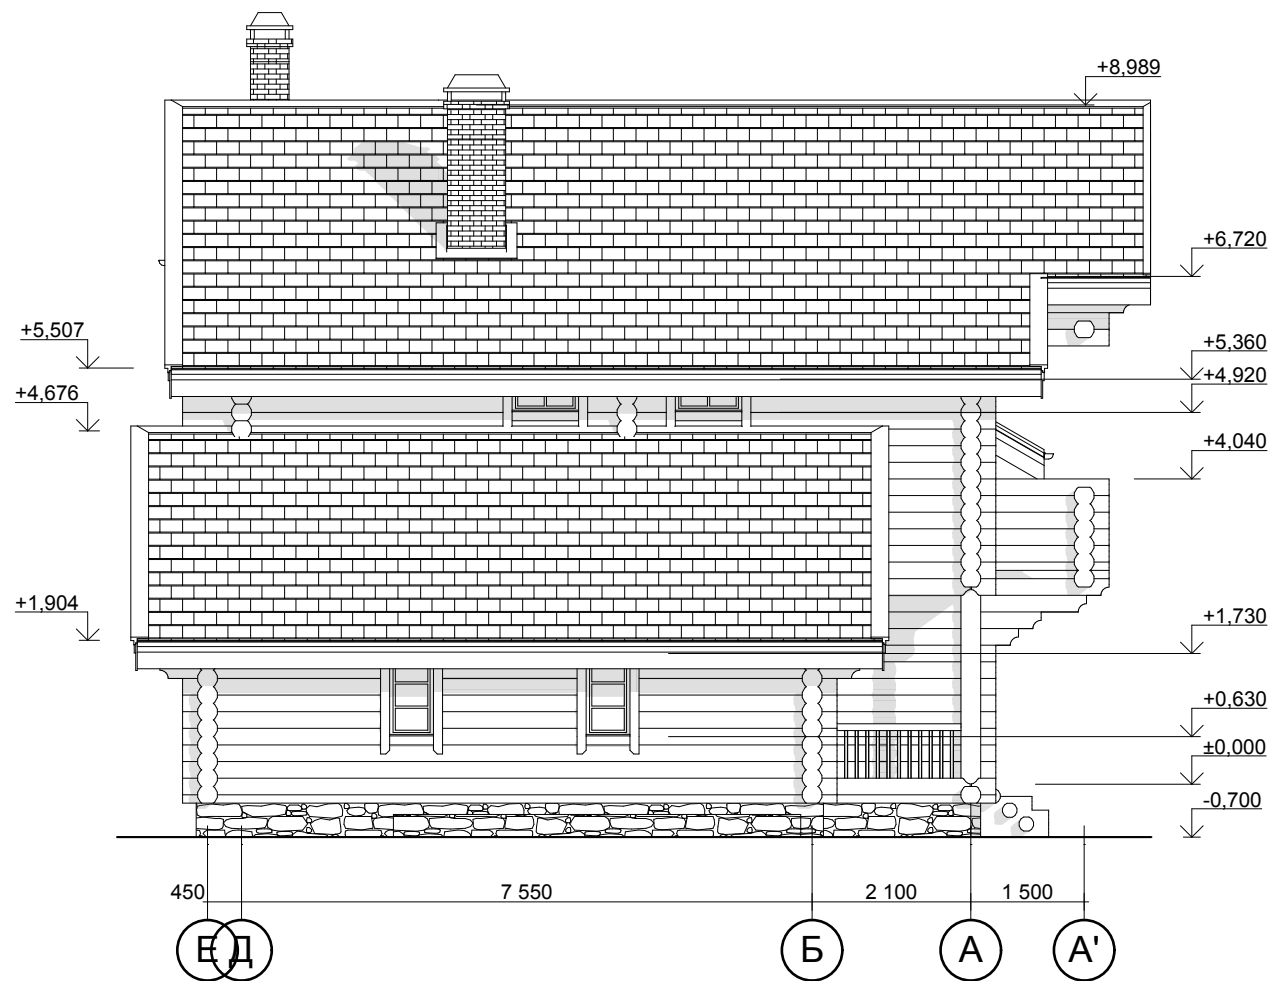


Фасад в осях Е-А'

Стадия	Лист	Листов
ЭП	12	21

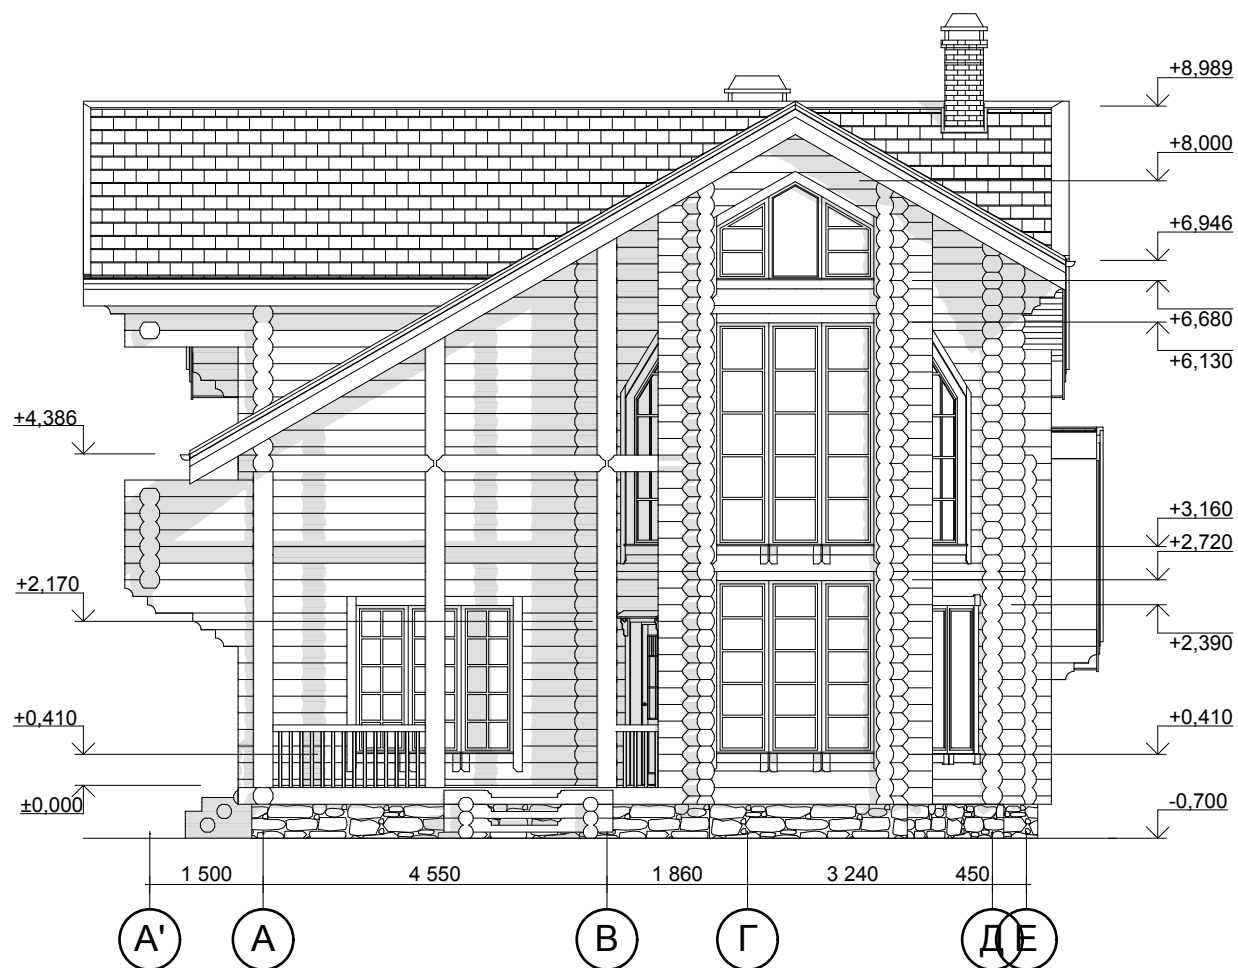


Фасад в осях А'-Е

Стадия	Лист	Листов
ЭП	13	21

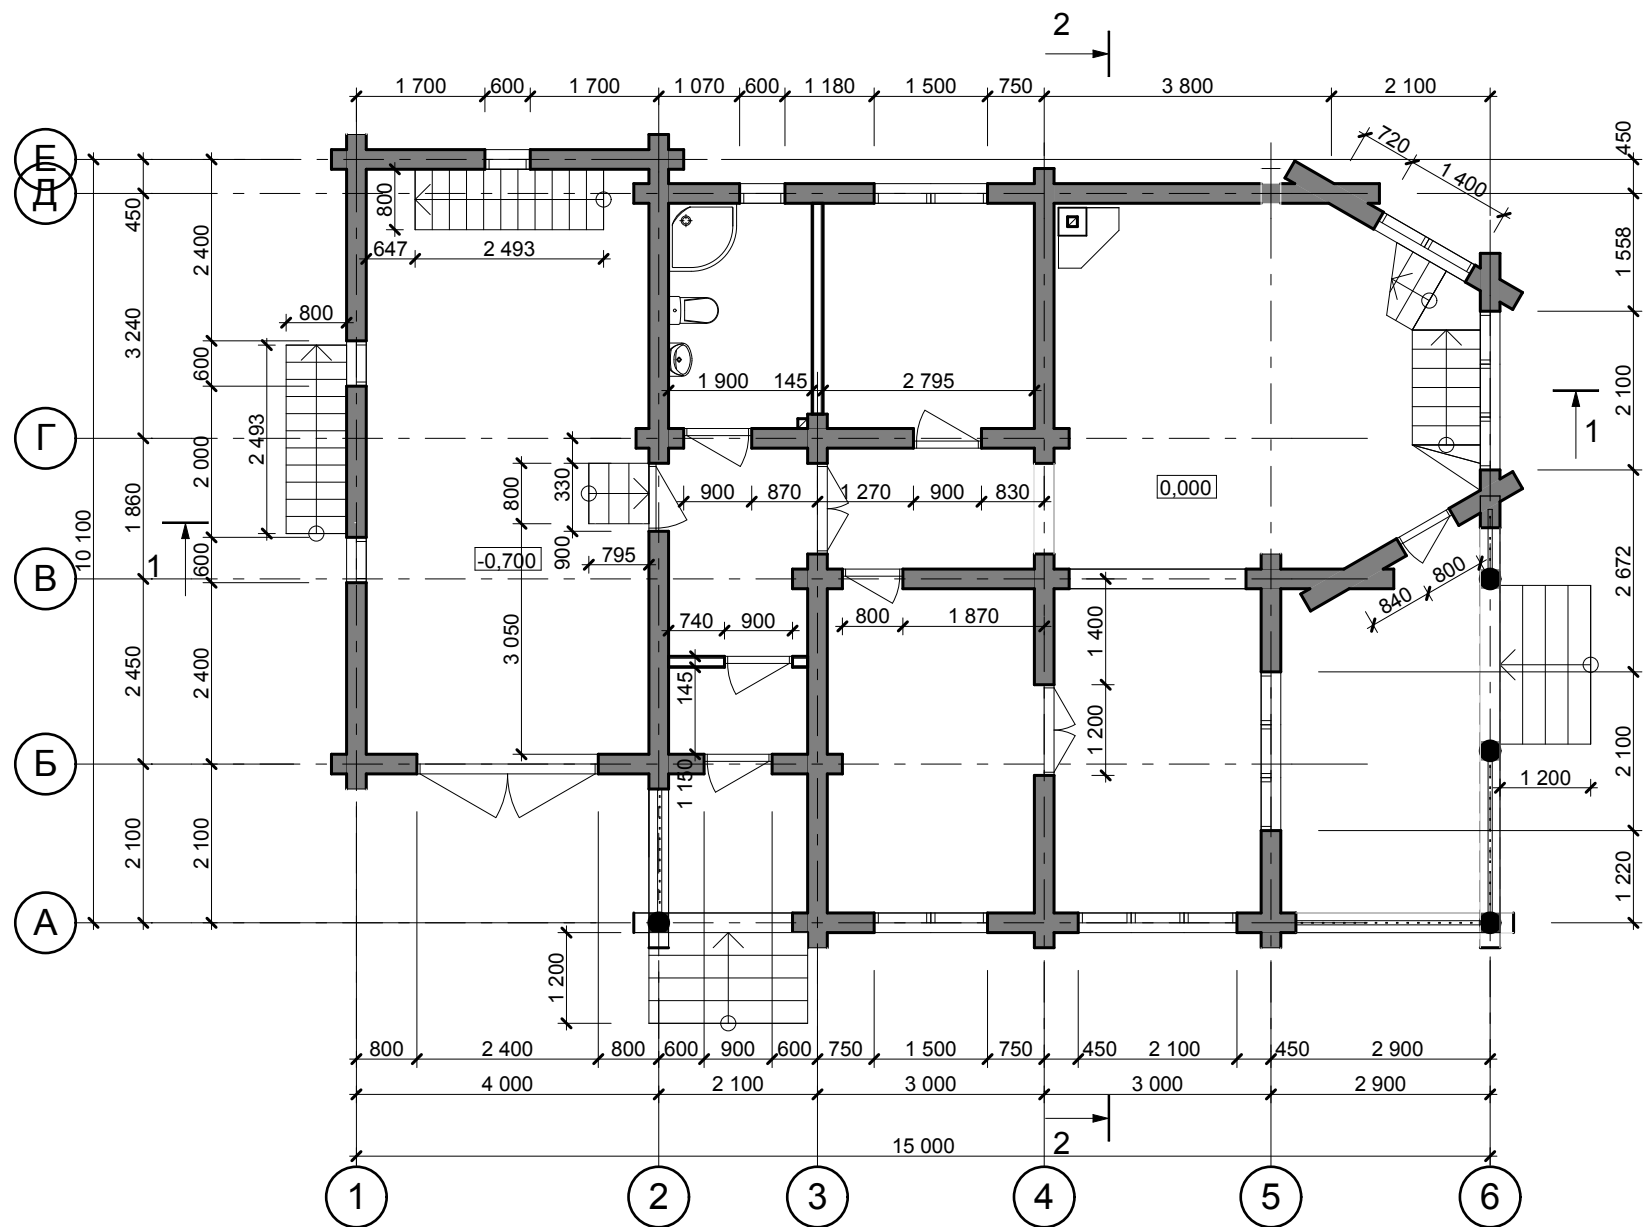

Кладочный план 1-го этажа


Стадия	Лист	Листов
ЭП	14	21

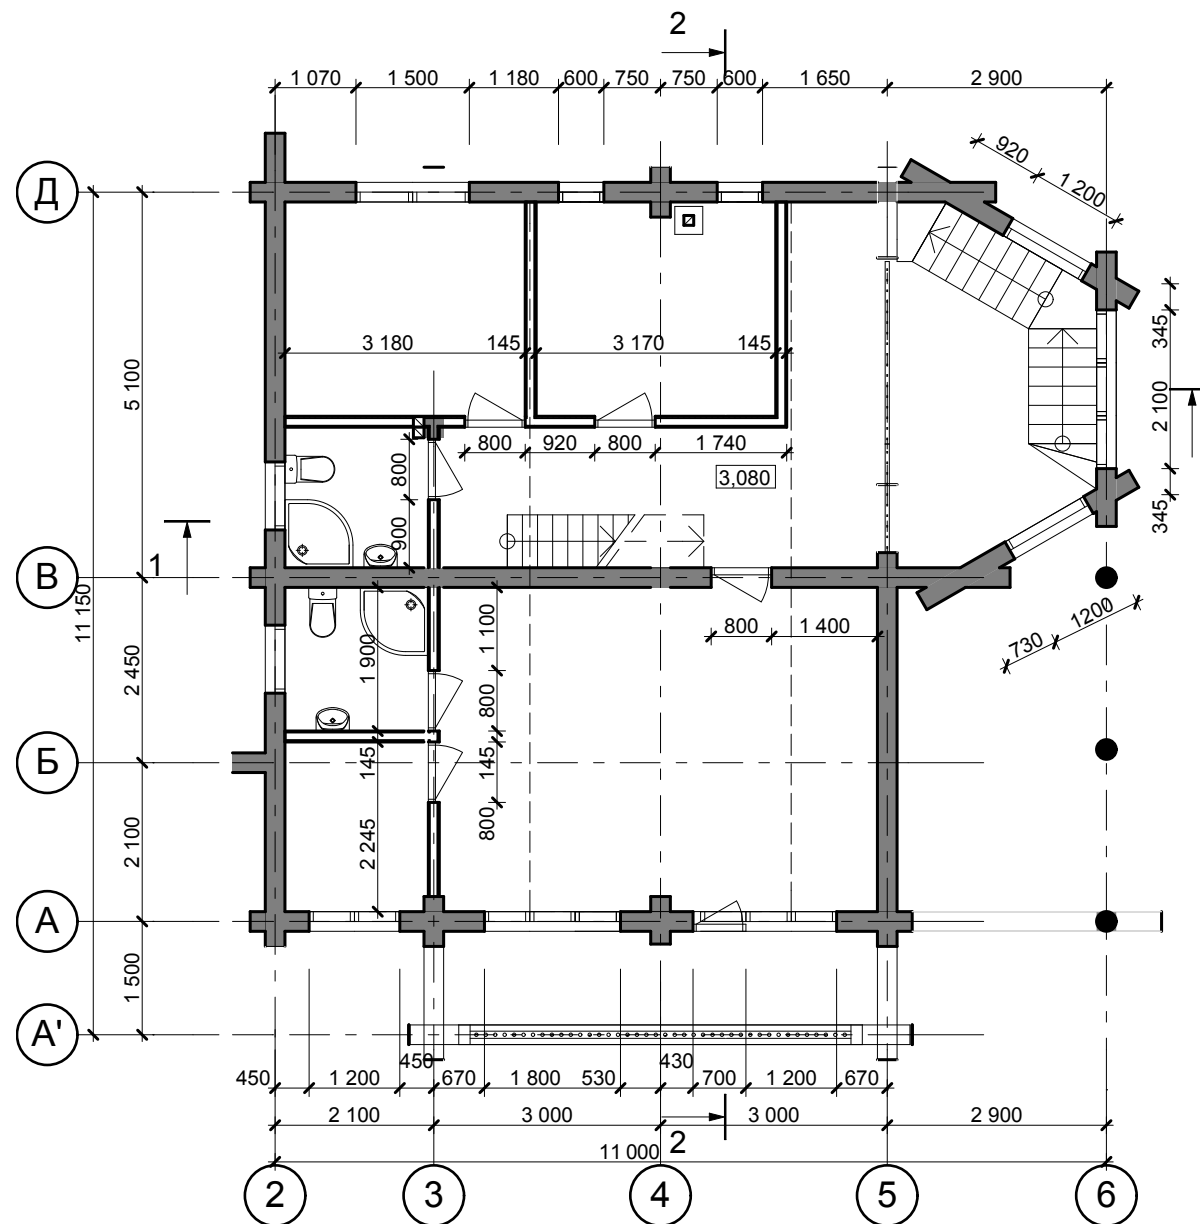


Кладочный план 2-го этажа

Стадия	Лист	Листов
ЭП	15	21

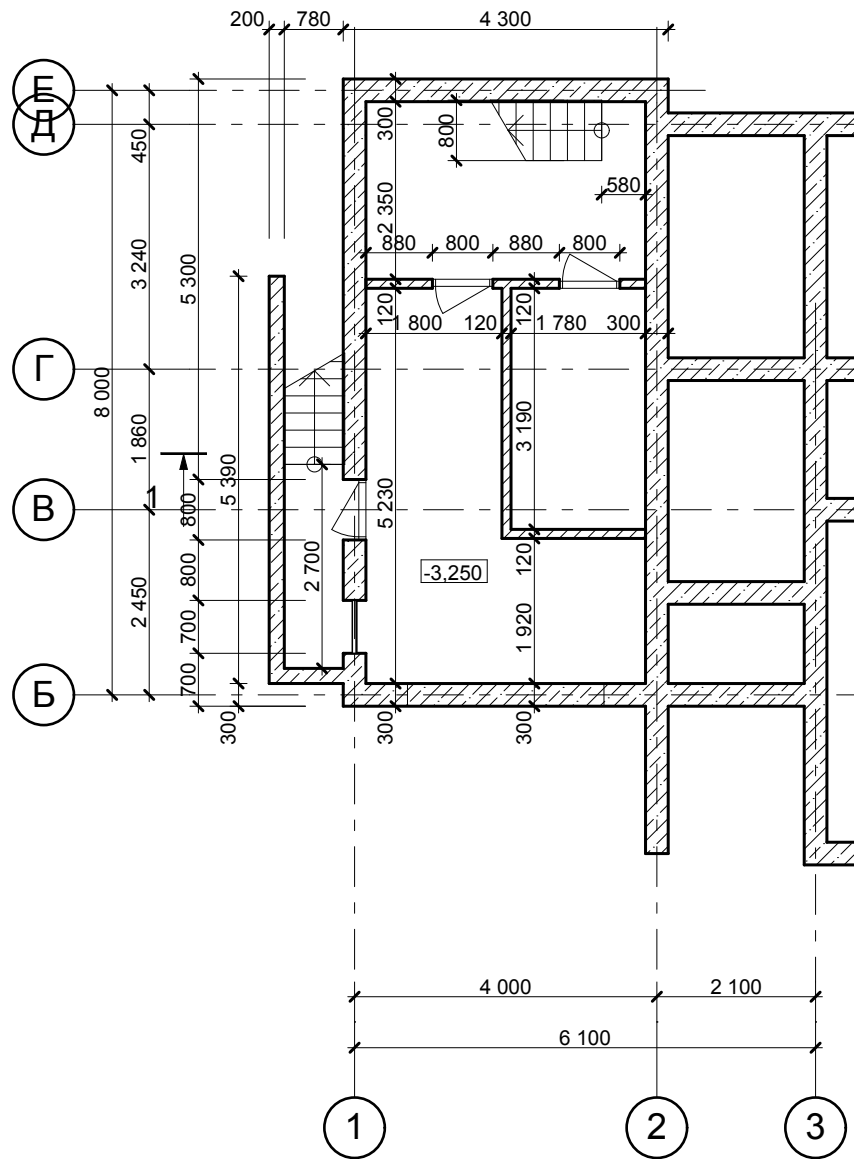Кладочный план подвала




Кладочный план на отметке +6,080

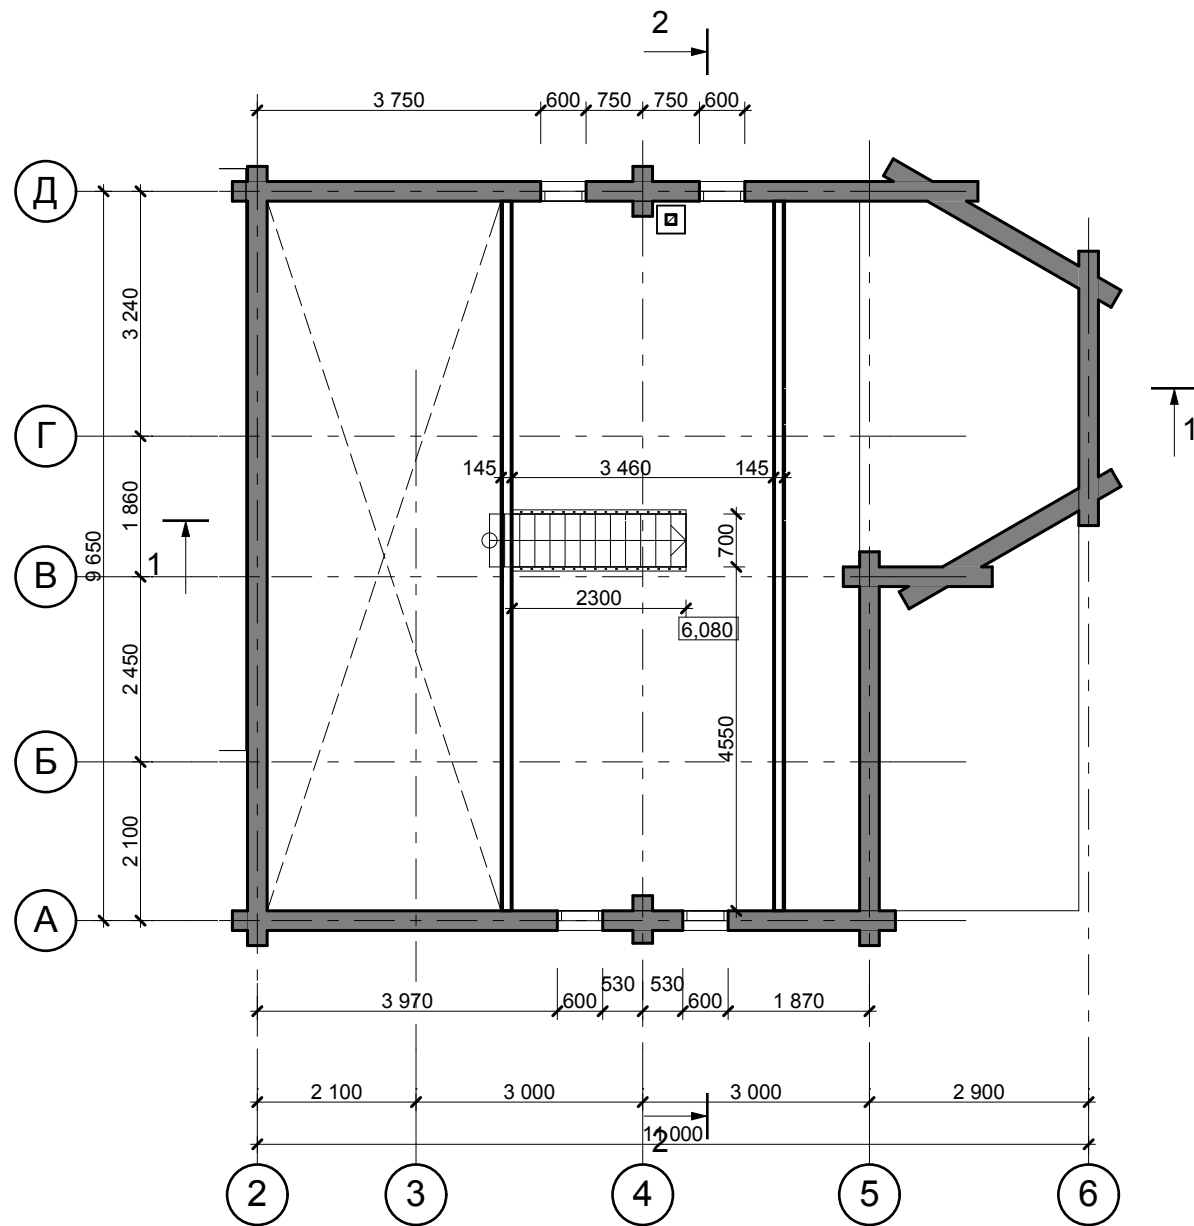


Клад. план подвала, на отметке +6,080

Стадия	Лист	Листов
ЭП	16	21

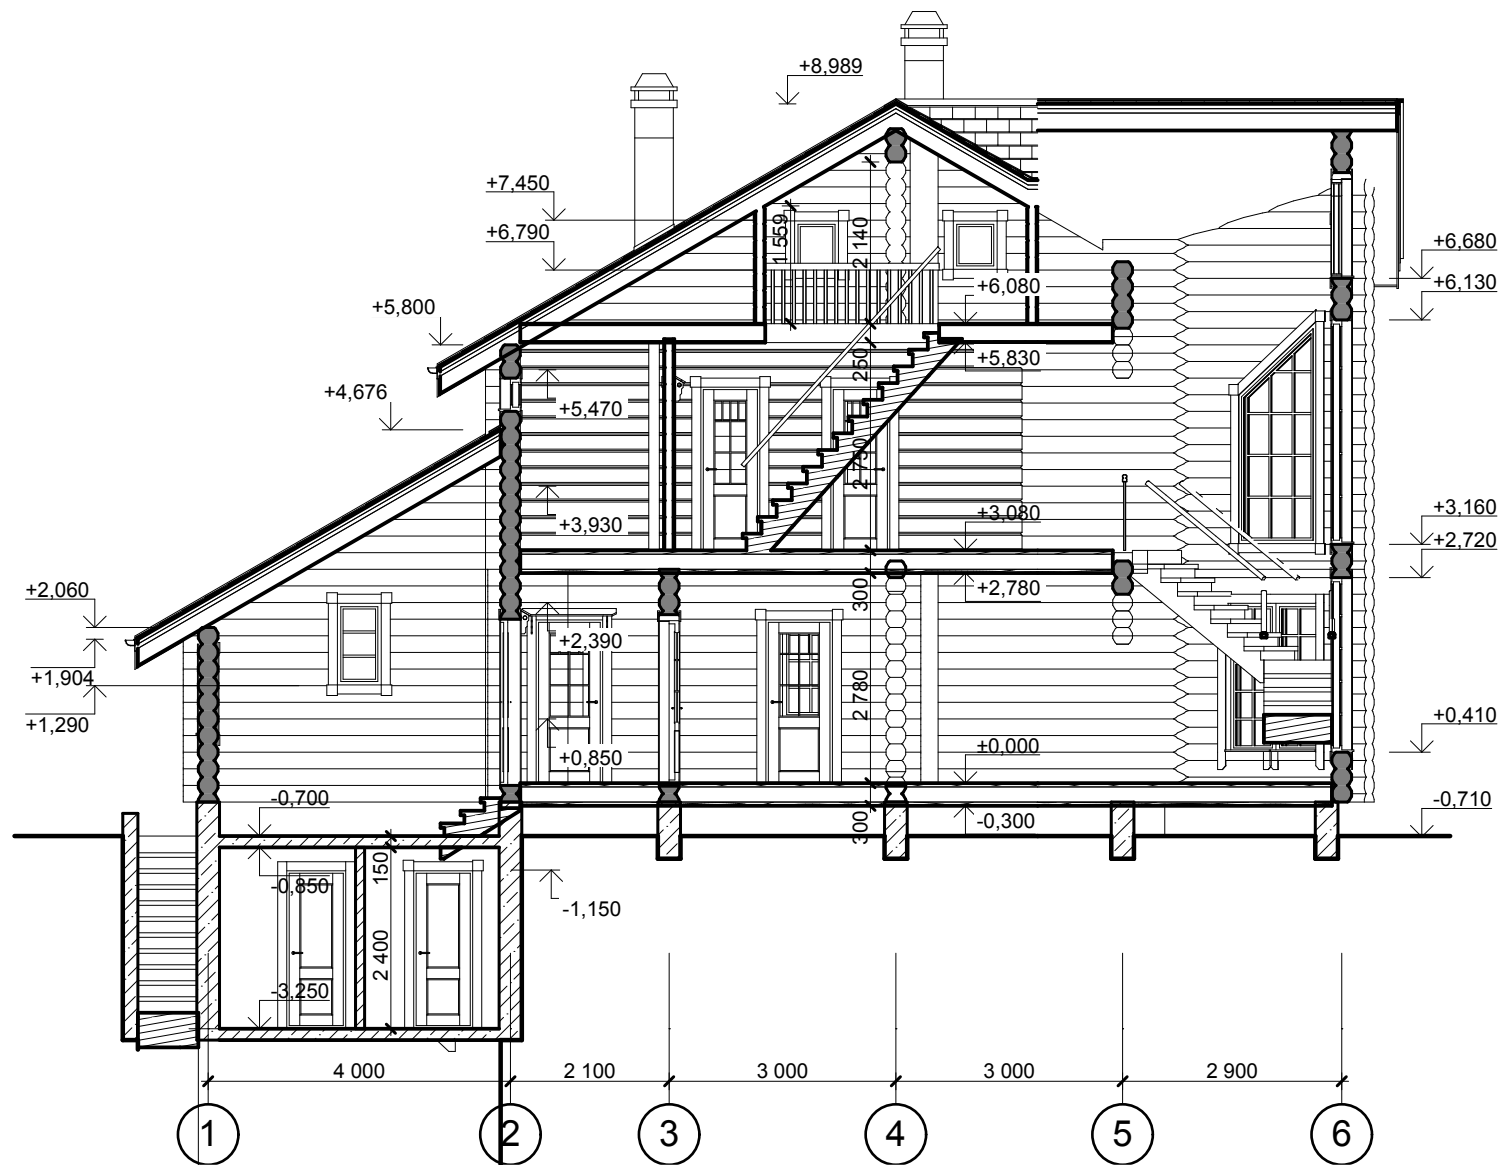

Разрез 1-1


Стадия	Лист	Листов
ЭП	17	21



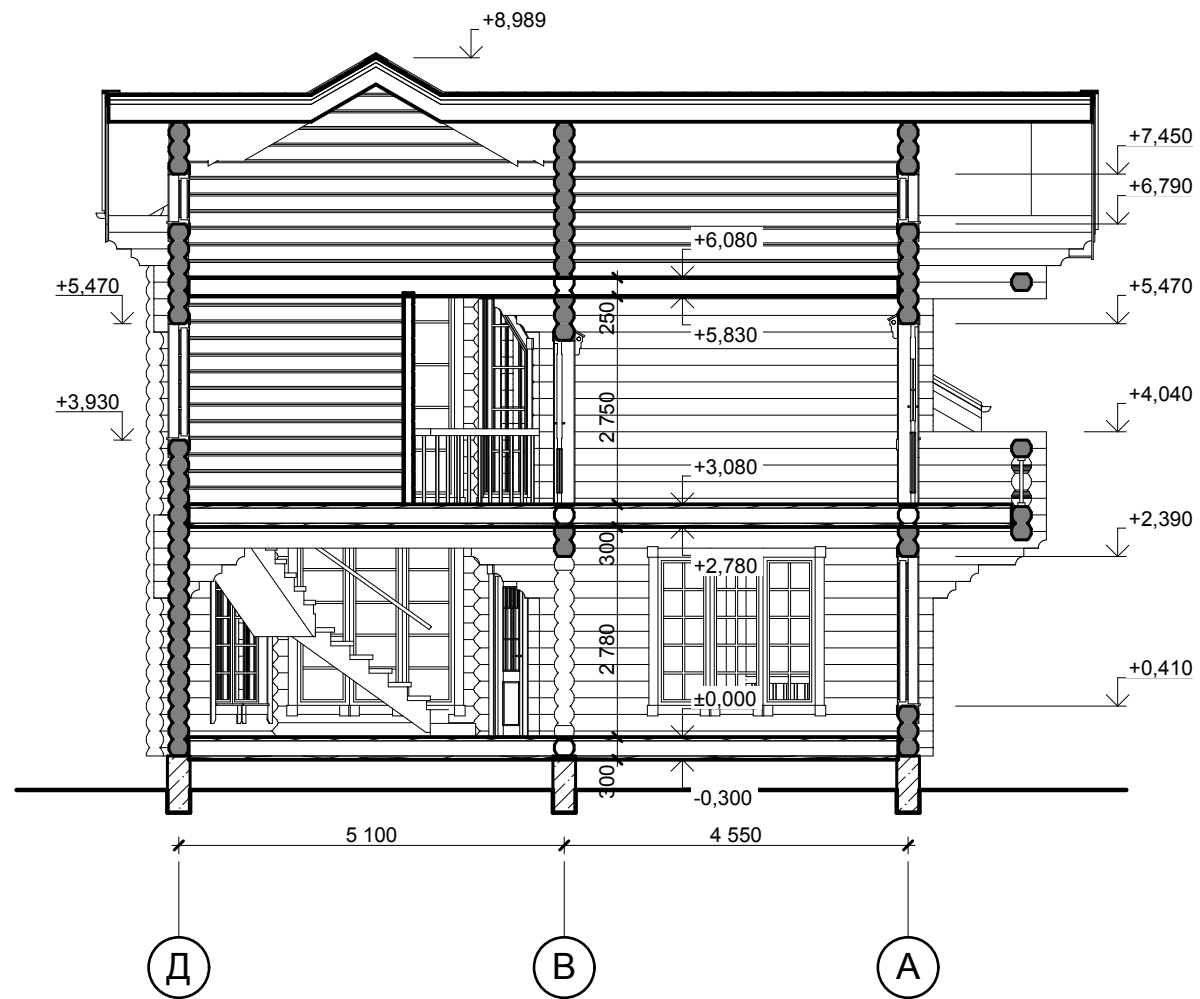


Разрез 2-2

Стадия	Лист	Листов
ЭП	18	21







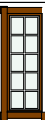
Смета окон

Количество	1	1	1	1	1	1	1	1	1	1	1	2
Размер Ш х В	600x1 100	700x1 124	700x1 124	700x1 320	700x1 980	700x2 310	700x2 970	900x440	900x440	1 200x2 9..	1 200x2 9..	600x660
Ориентация	Л	Л	П	П	П	П	Л	Л	П	Л	П	Л
3D-фронтал...												

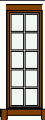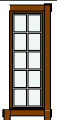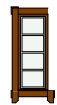Количество	2	2	2	2	3	3	3	4	5	5
Размер Ш х В	600x660	600x1 100	700x2 310	700x2 970	700x1 980	750x1 540	750x1 540	700x1 980	600x1 540	600x1 540
Ориентация	П	П	Л	П	П	Л	П	Л	Л	П
3D-фронтал...										

Смета окон

Стадия	Лист	Листов
ЭП	20	21

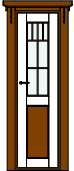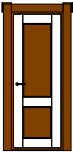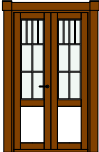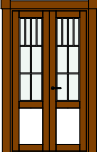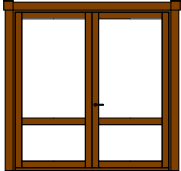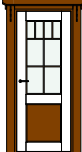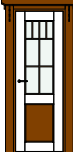Смета дверей										
Количество	1	1	1	1	1	2	2	2	3	5
Размер Ш ...	700x2 420	800x2 100	1 200x2 150	1 200x2 200	2 400x2 430	800x2 100	900x2 200	900x2 200	800x2 200	800x2 200
Ориентация	П	П	Л	П	П	Л	Л	П	П	Л
3D-фронта...										
								Стадия	Лист	Листов
								ЭП	21	21