

Эскизный проект жилого дома



ВЕДОМОСТЬ ЧЕРТЕЖЕЙ КОМПЛЕКТА ЭП

Лист	Наименование	Примечание
1	Титульный лист	
2	Общие данные	
3	Визуализация	
4	Визуализация	
5	Визуализация	
6	План 1-го этажа	
7	План 2-го этажа	
8	Кладочный план 1-го и 2-го этажа	
9	Фасад 1-4,Г-А	
10	Фасад А-Г, 4-1	
11	Разрез 1-1, 2-2	
12	План кровли	
13	Смета окон и дверей	

Технико-экономические показатели

п/п	Наименование	Количество, ед. измер.
1	Площадь участка	- м²
2	Жилая площадь	46,71 м²
3	Общая площадь	104,79 м²
4	Площадь застройки	81,48 м²
5	Строительный объем	251,24 м³
6	Этажность	2


Технико-экономические показатели		
п/п	Наименование	Количество, ед. измер.
1	Площадь участка	- м ²
2	Жилая площадь	46,71 м ²
3	Общая площадь	104,79 м ²
4	Площадь застройки	81,48 м ²
5	Строительный объем	251,24 м ³
6	Этажность	2

Общие данные	Стадия	Лист	Листов
	ЭП	2	13









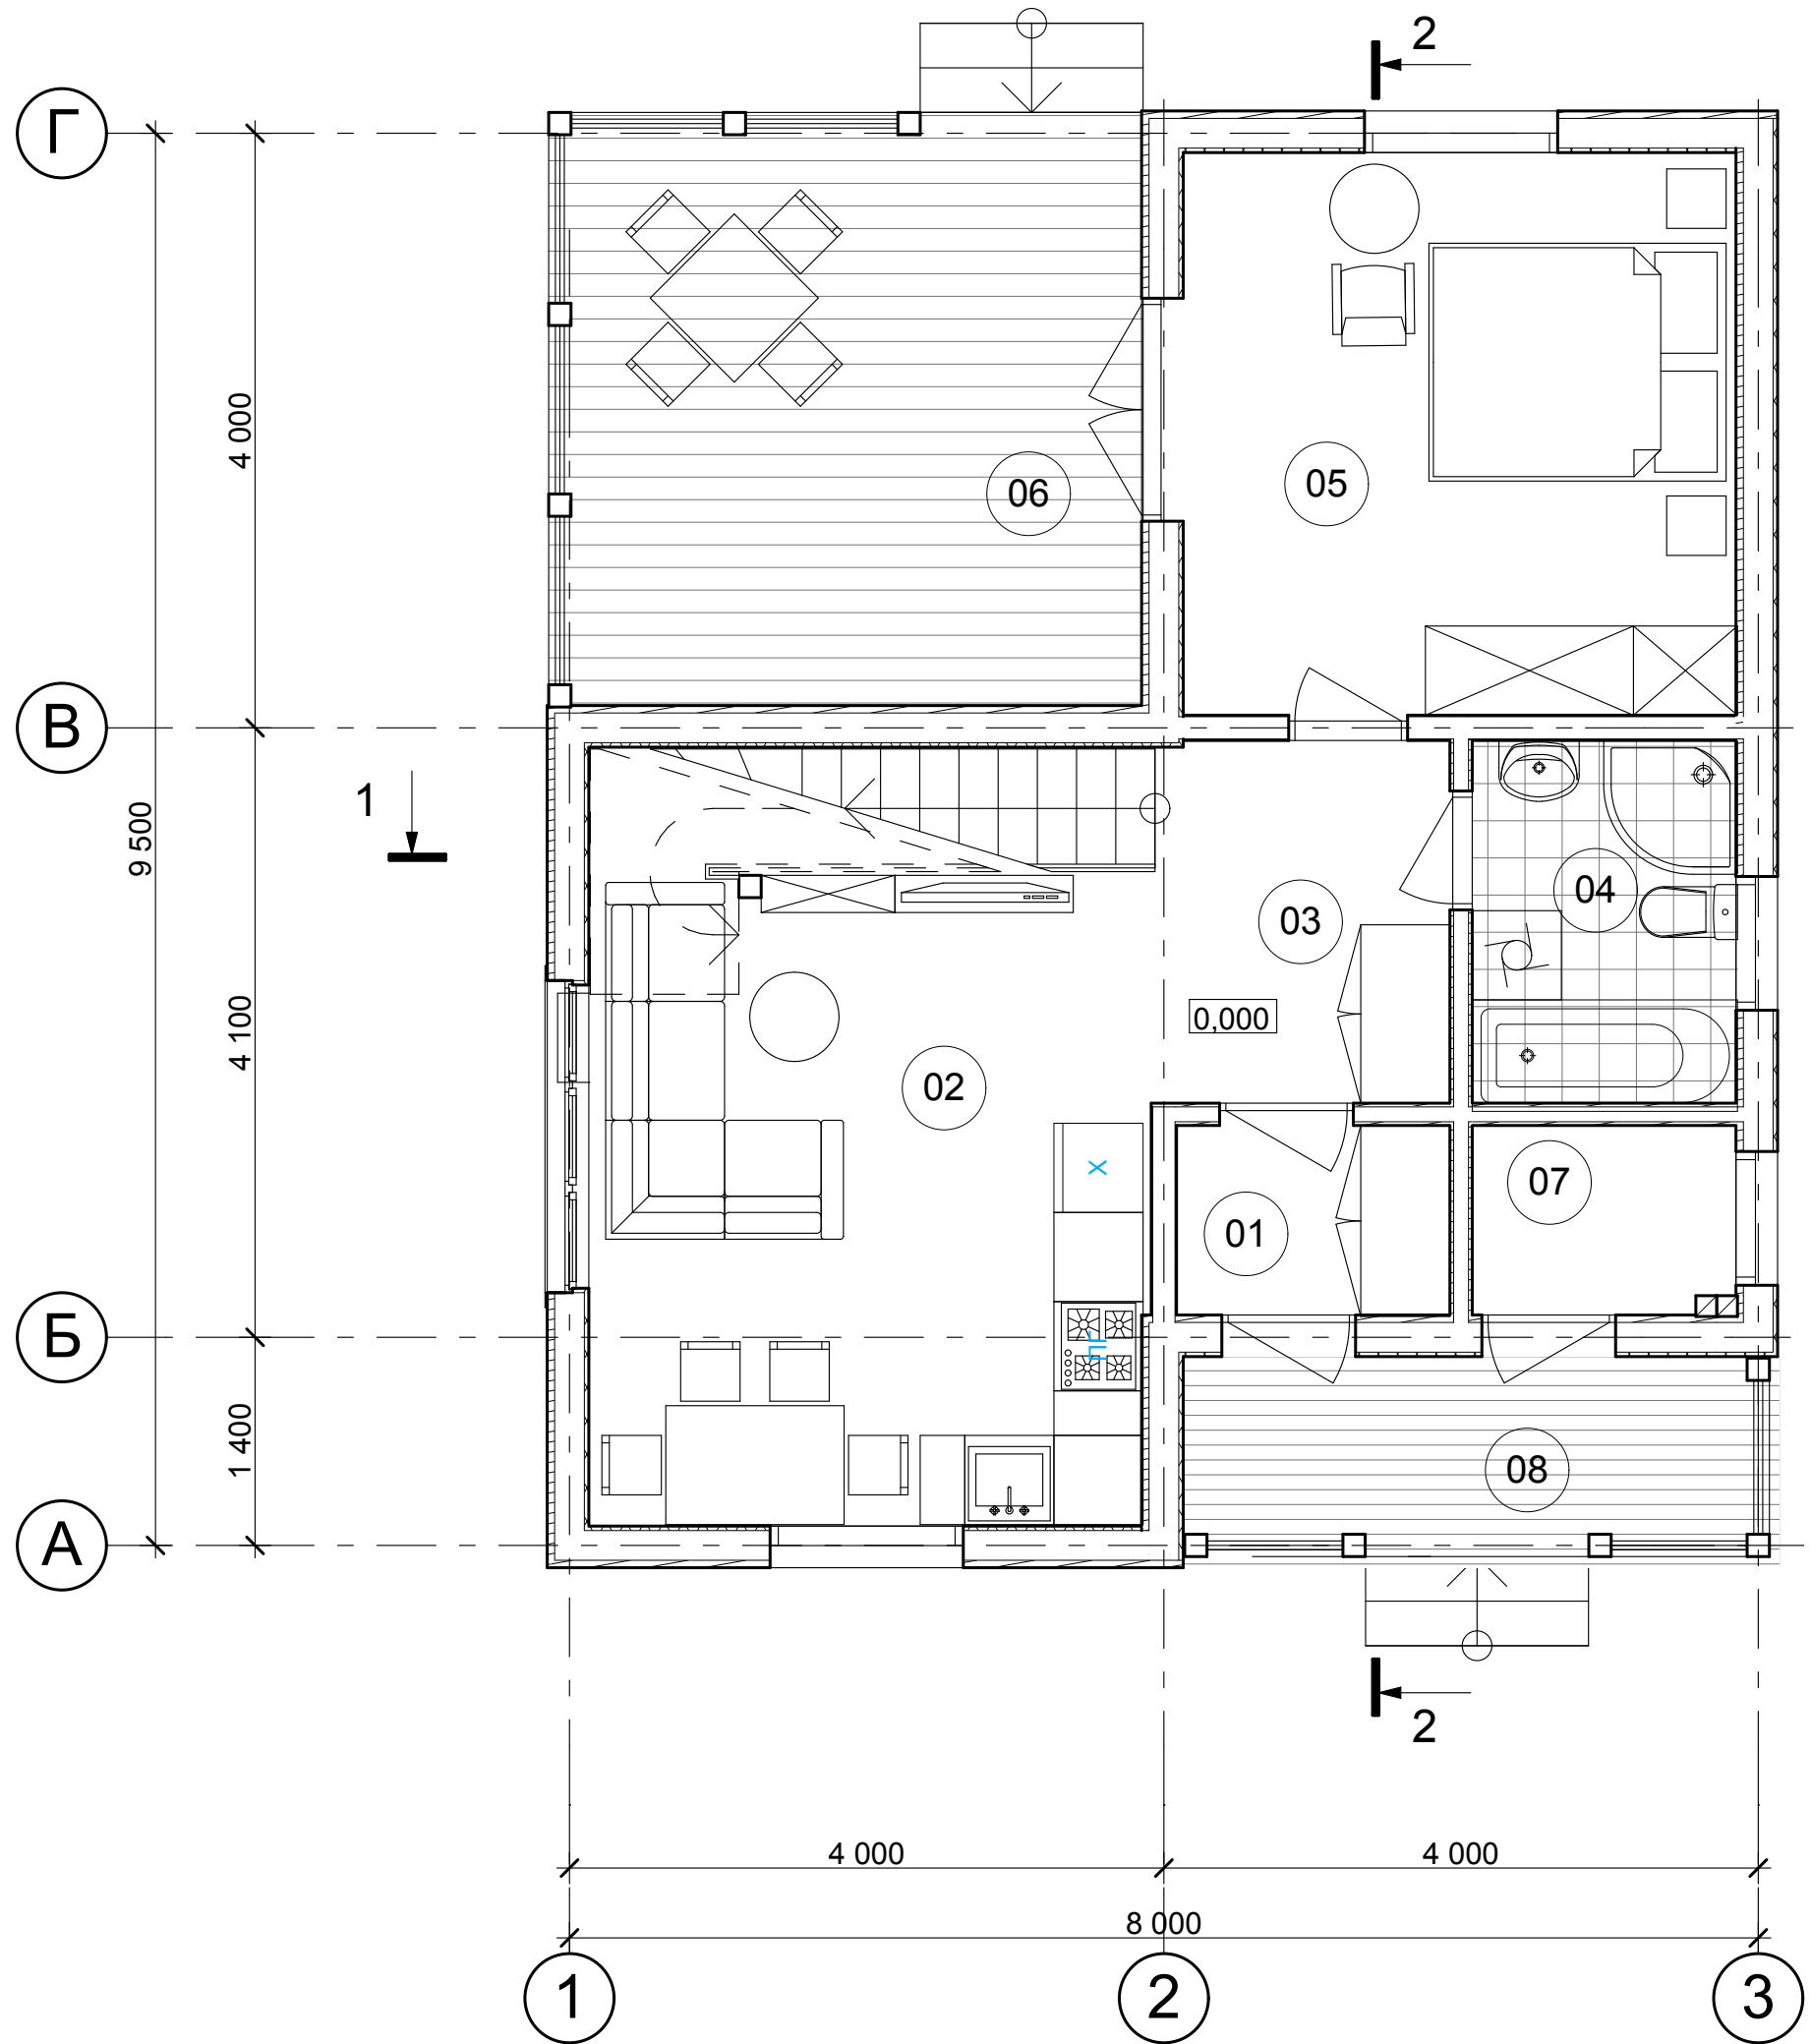


Экспликация помещений 1-го этажа			
№п/п	Наименование	Площад, м кв	Кат.
01	Тамбур	2,36	
02	Гостиная-кухня	19,84	
03	Холл	4,90	
04	С/у	4,36	
05	Спальня	14,04	
06	Терраса	16,00	
07	Бойлерная	2,29	
08	Крыльцо	5,60	
		69,39 м2	

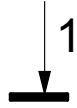


Экспликация помещений 2-го этажа			
№п/п	Наименование	Площад, м кв	Кат.
01	Комната отдыха	16,97	
02	Спальня	12,83	
03	Балкон	5,60	
		35,40 м2	

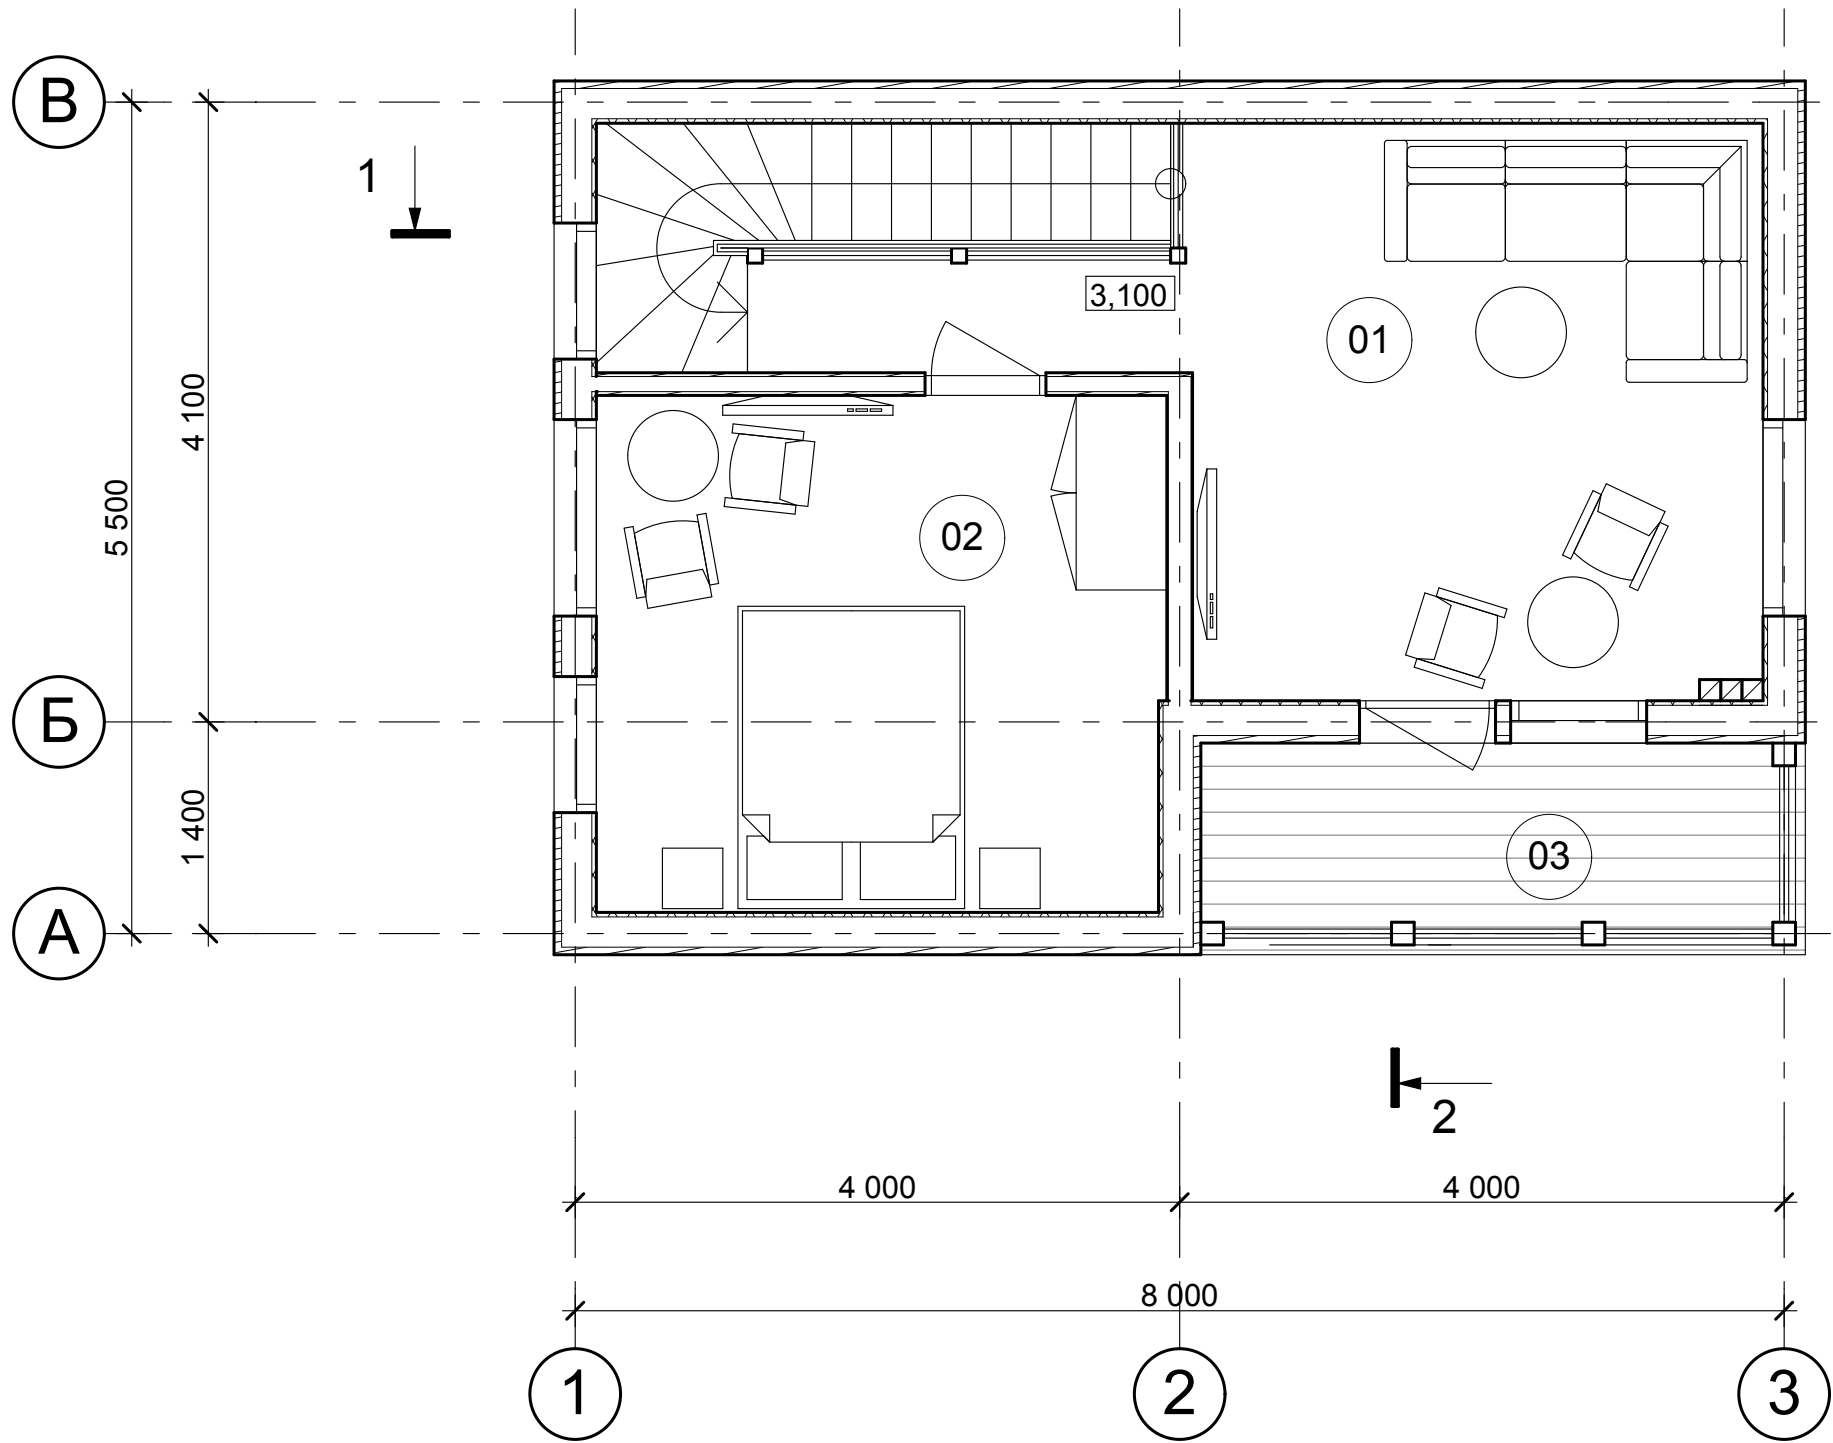


Кладочный план 1-го этажа (М 1:75)

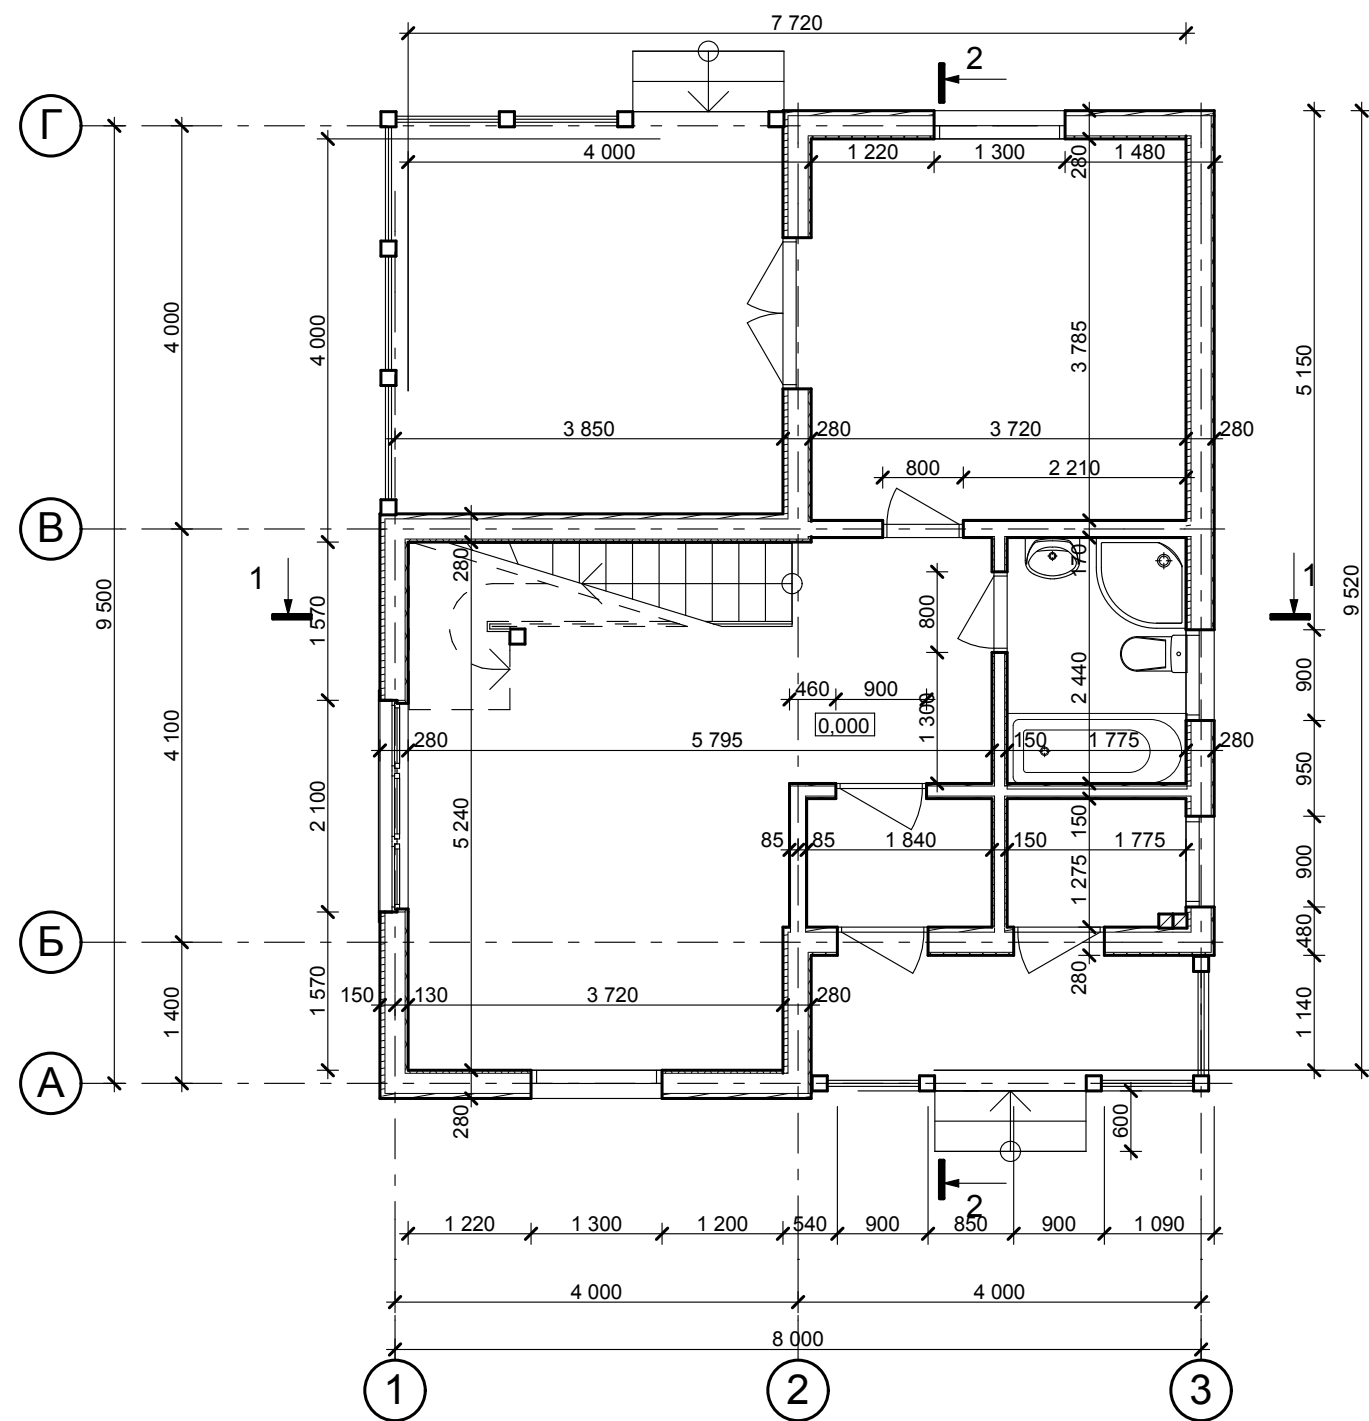

Кладочный план 2-го этажа (М 1:75)


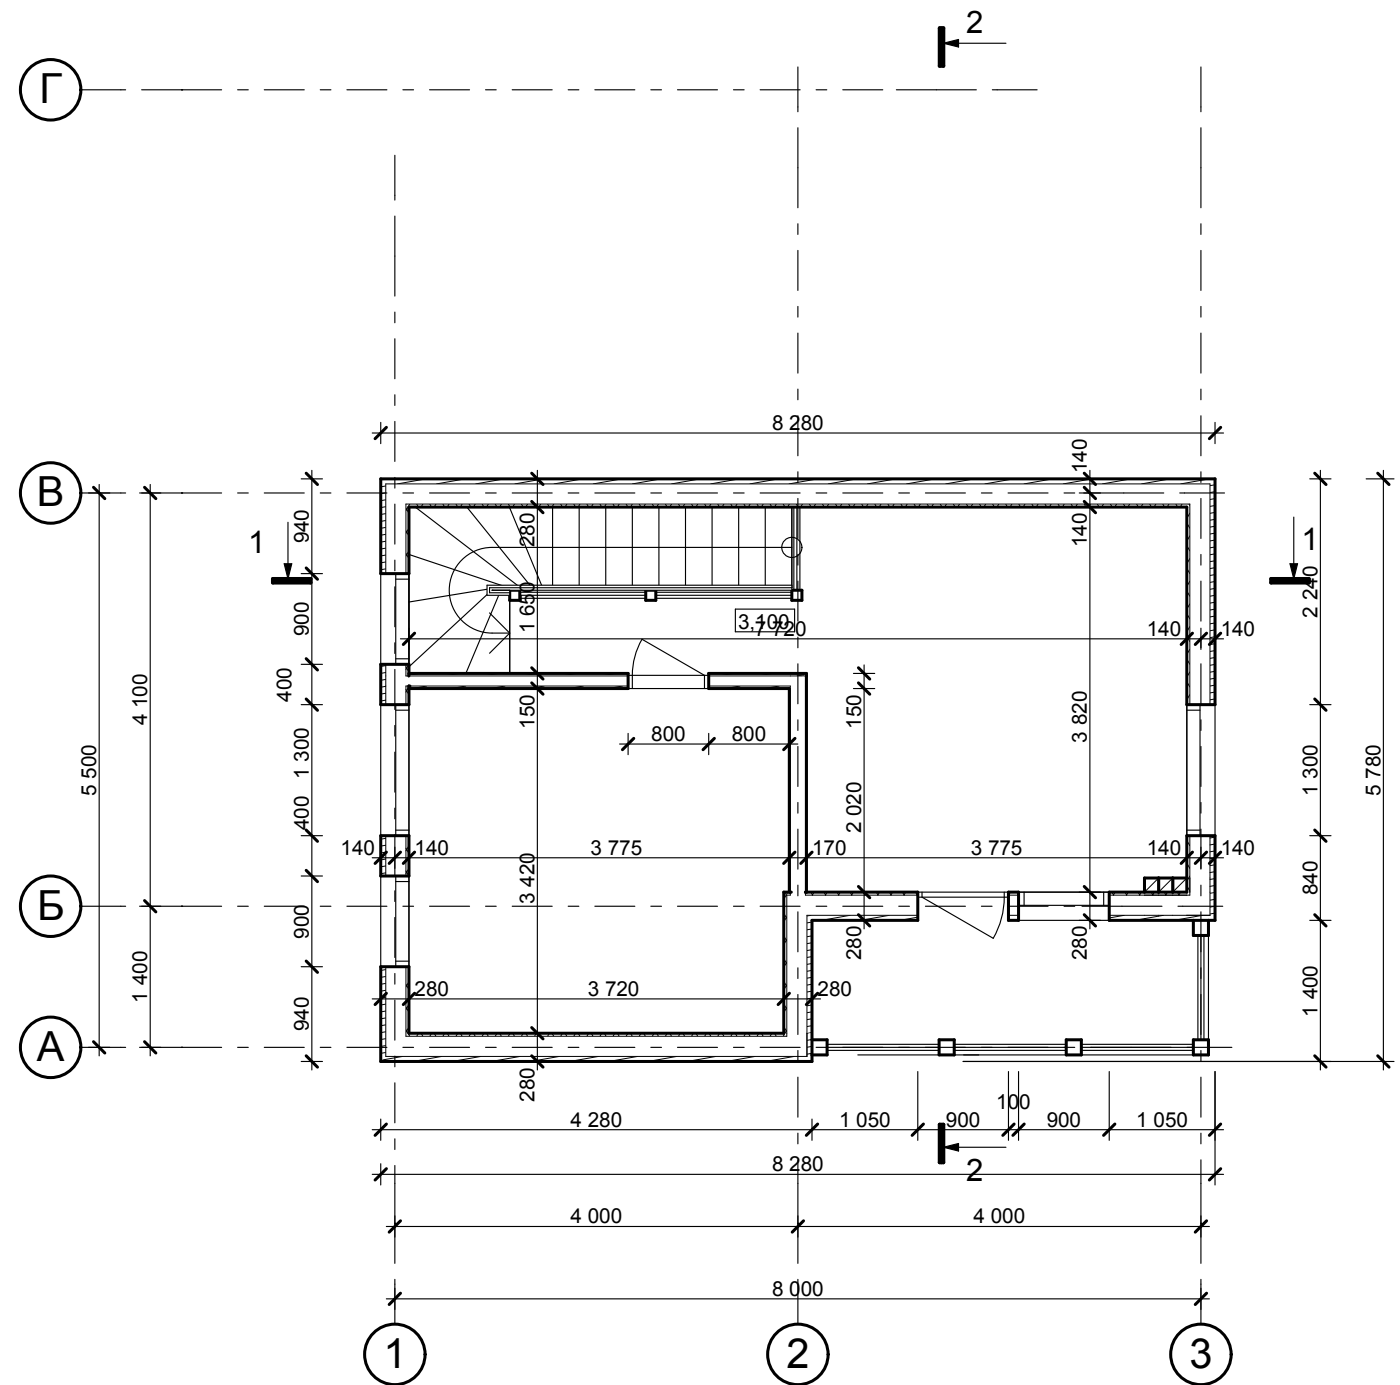


Фасад 1-4

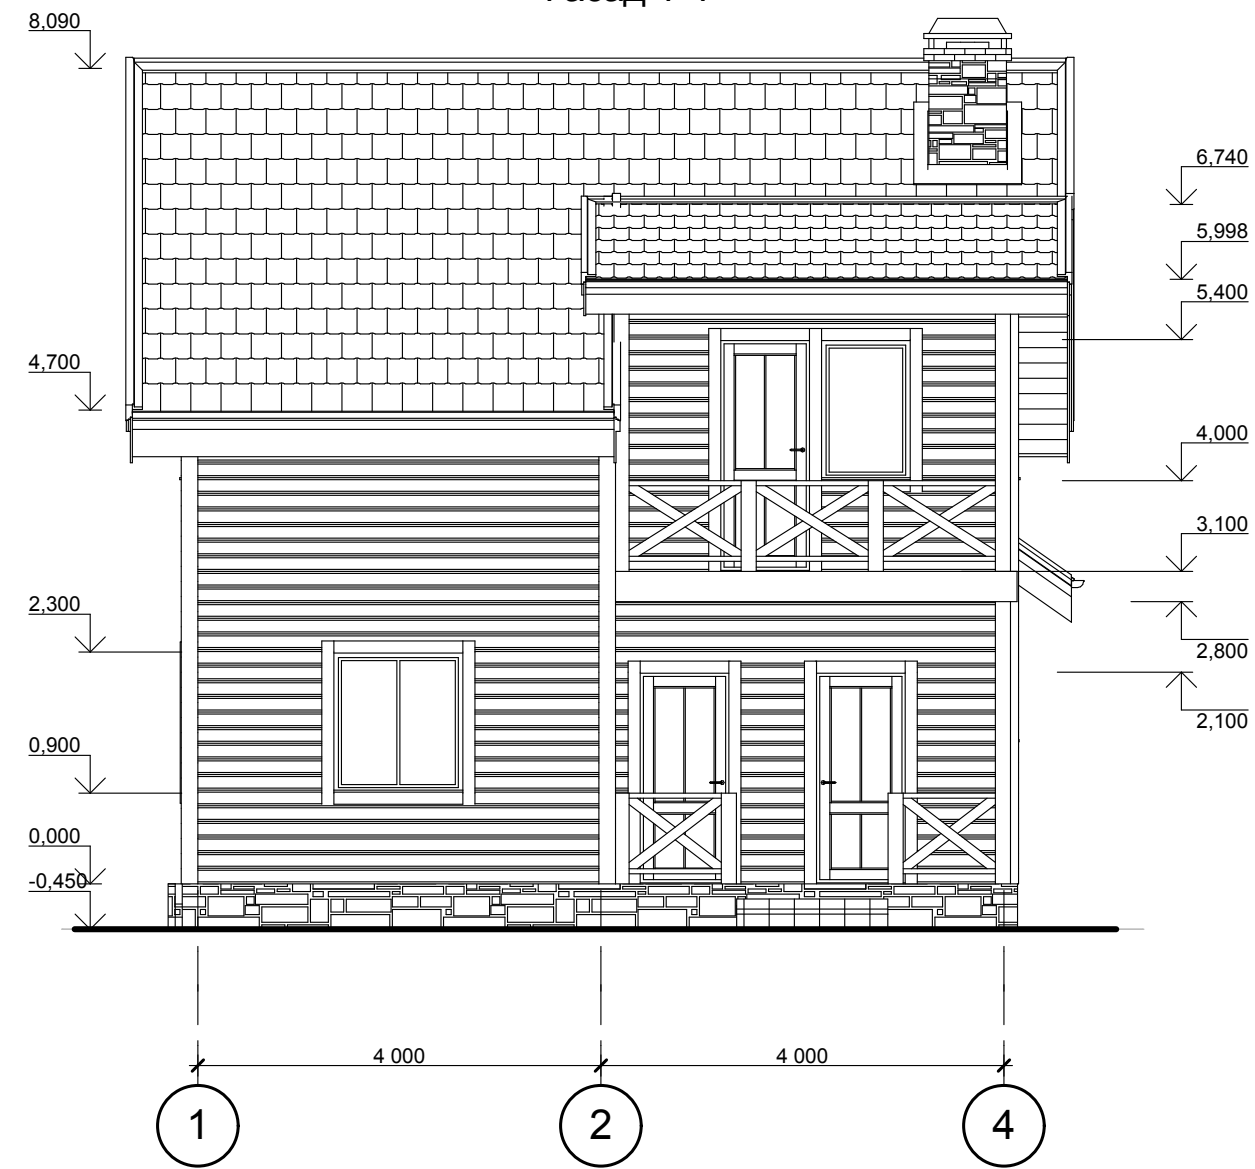


Фасад Г-А




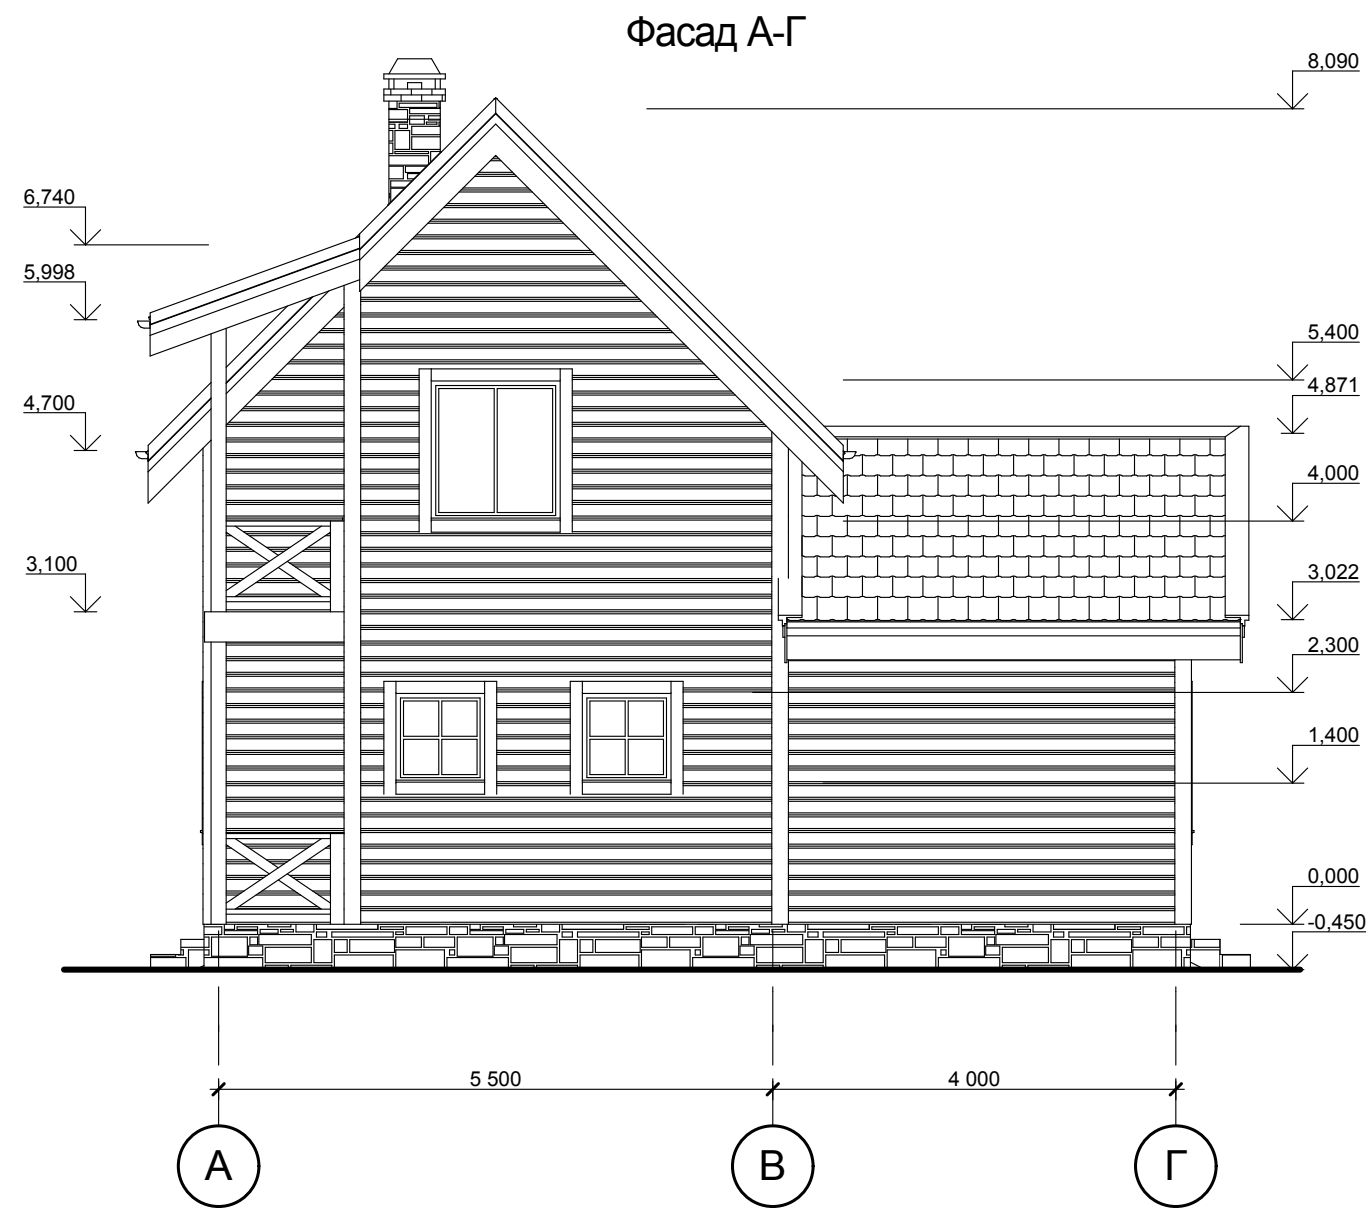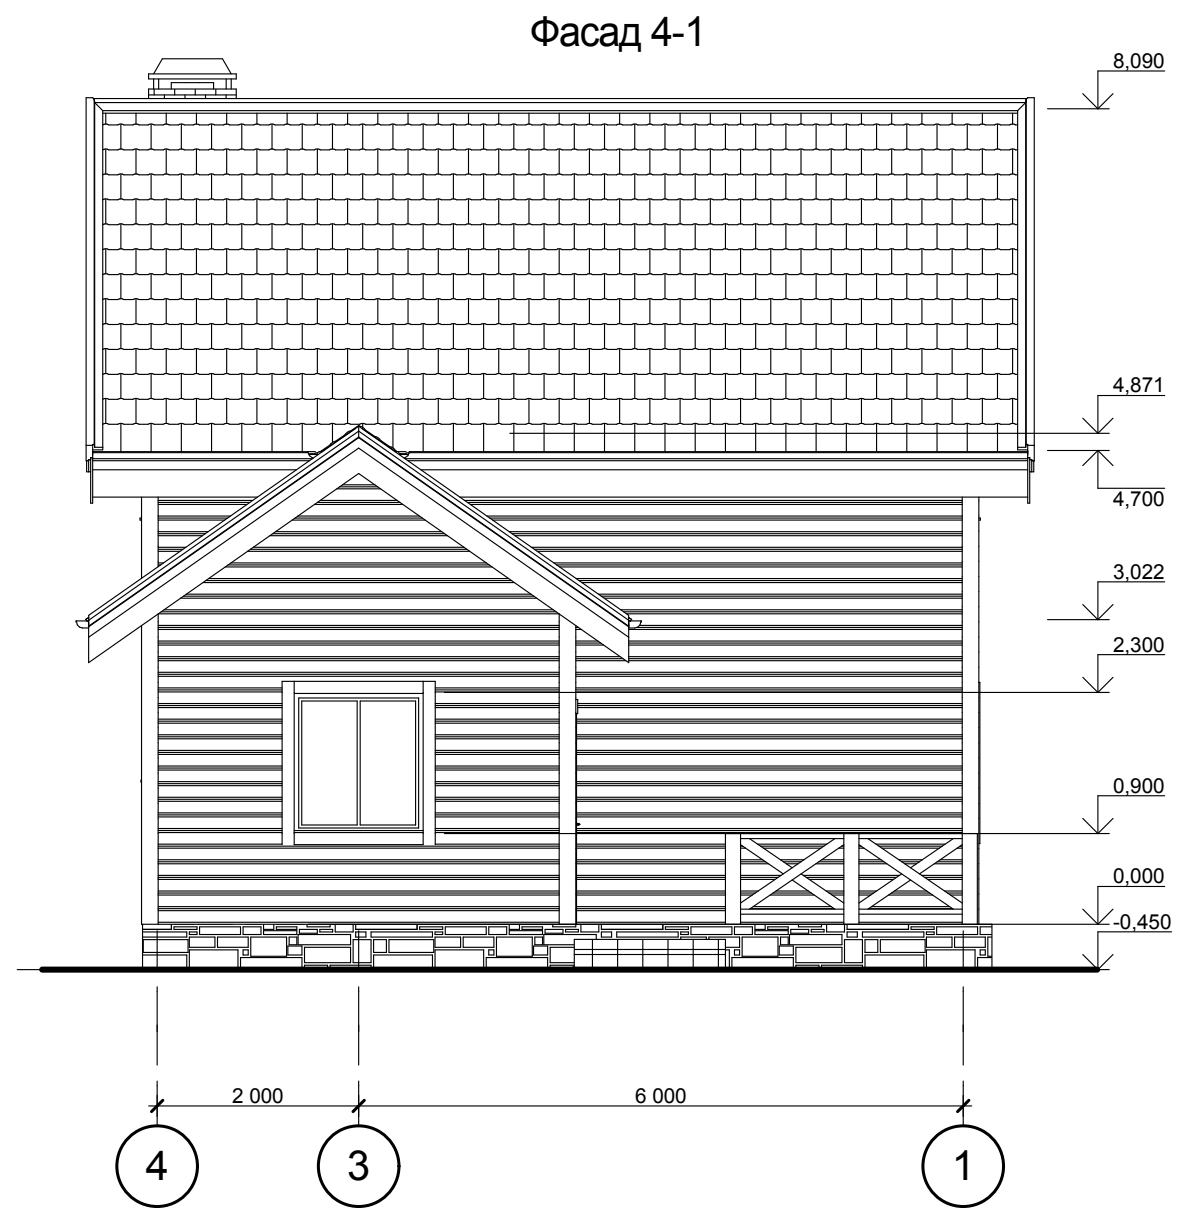


Разрез 1-1 (М 1:75)

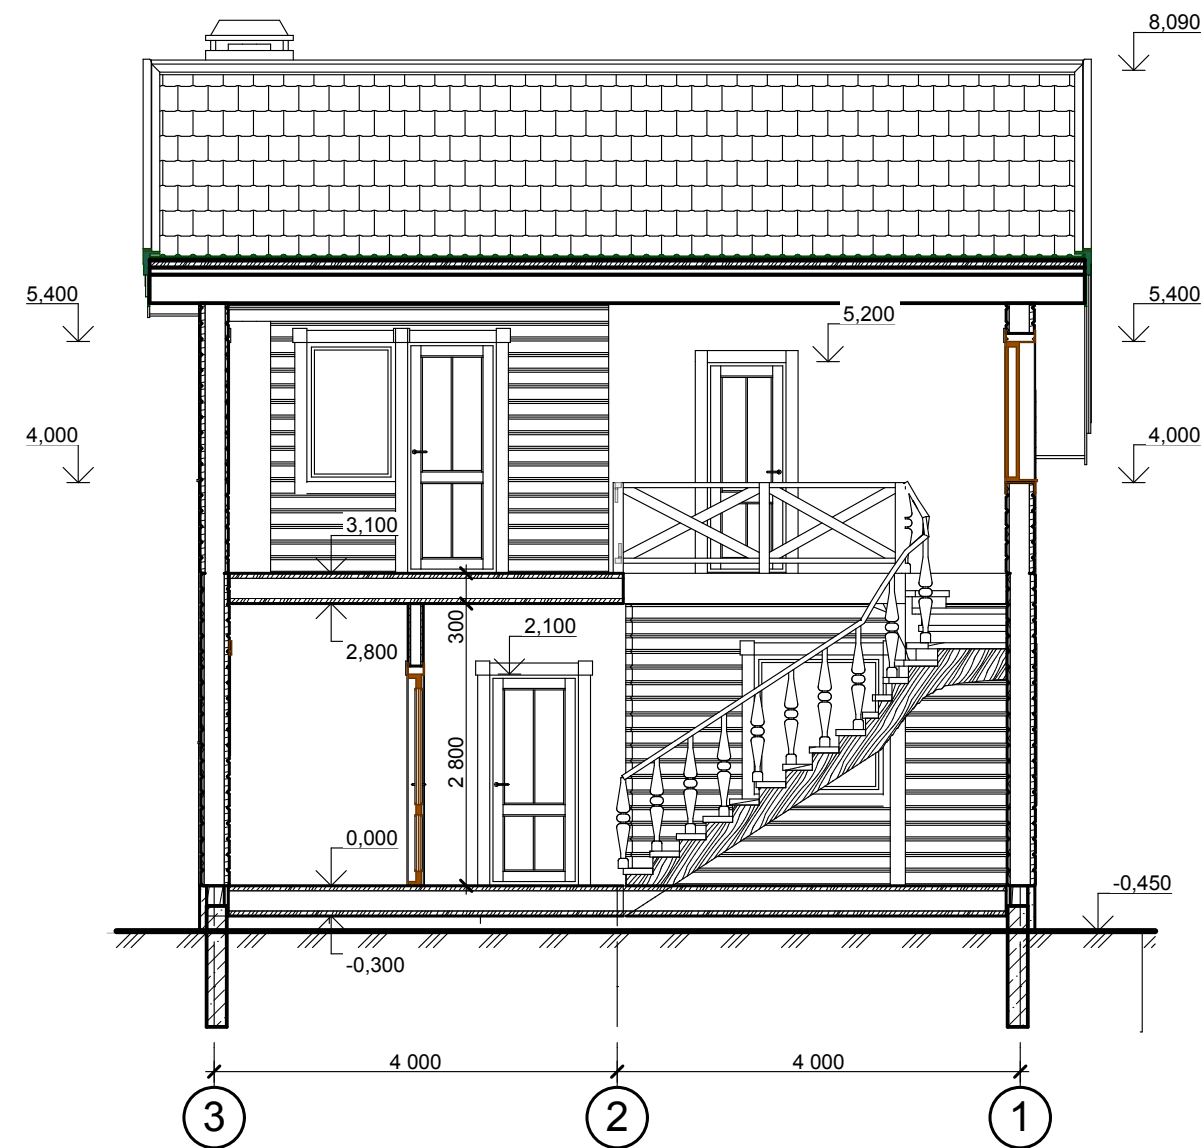







Разрез 2-2 (М 1:75)





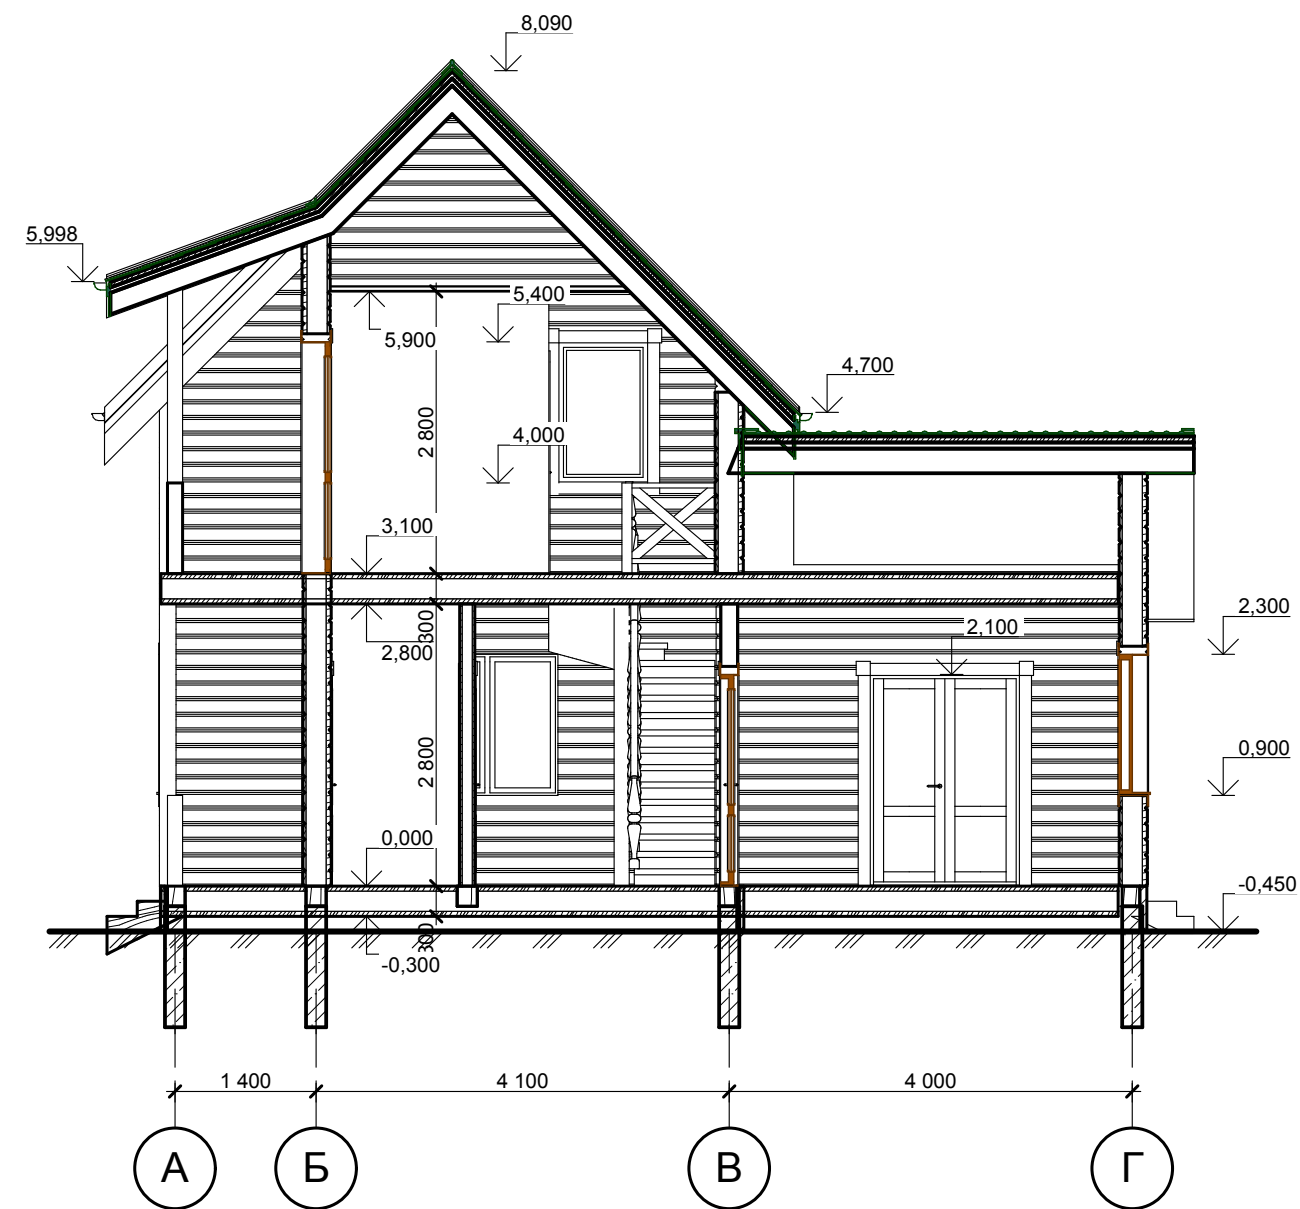


План кровли (М 1:75)

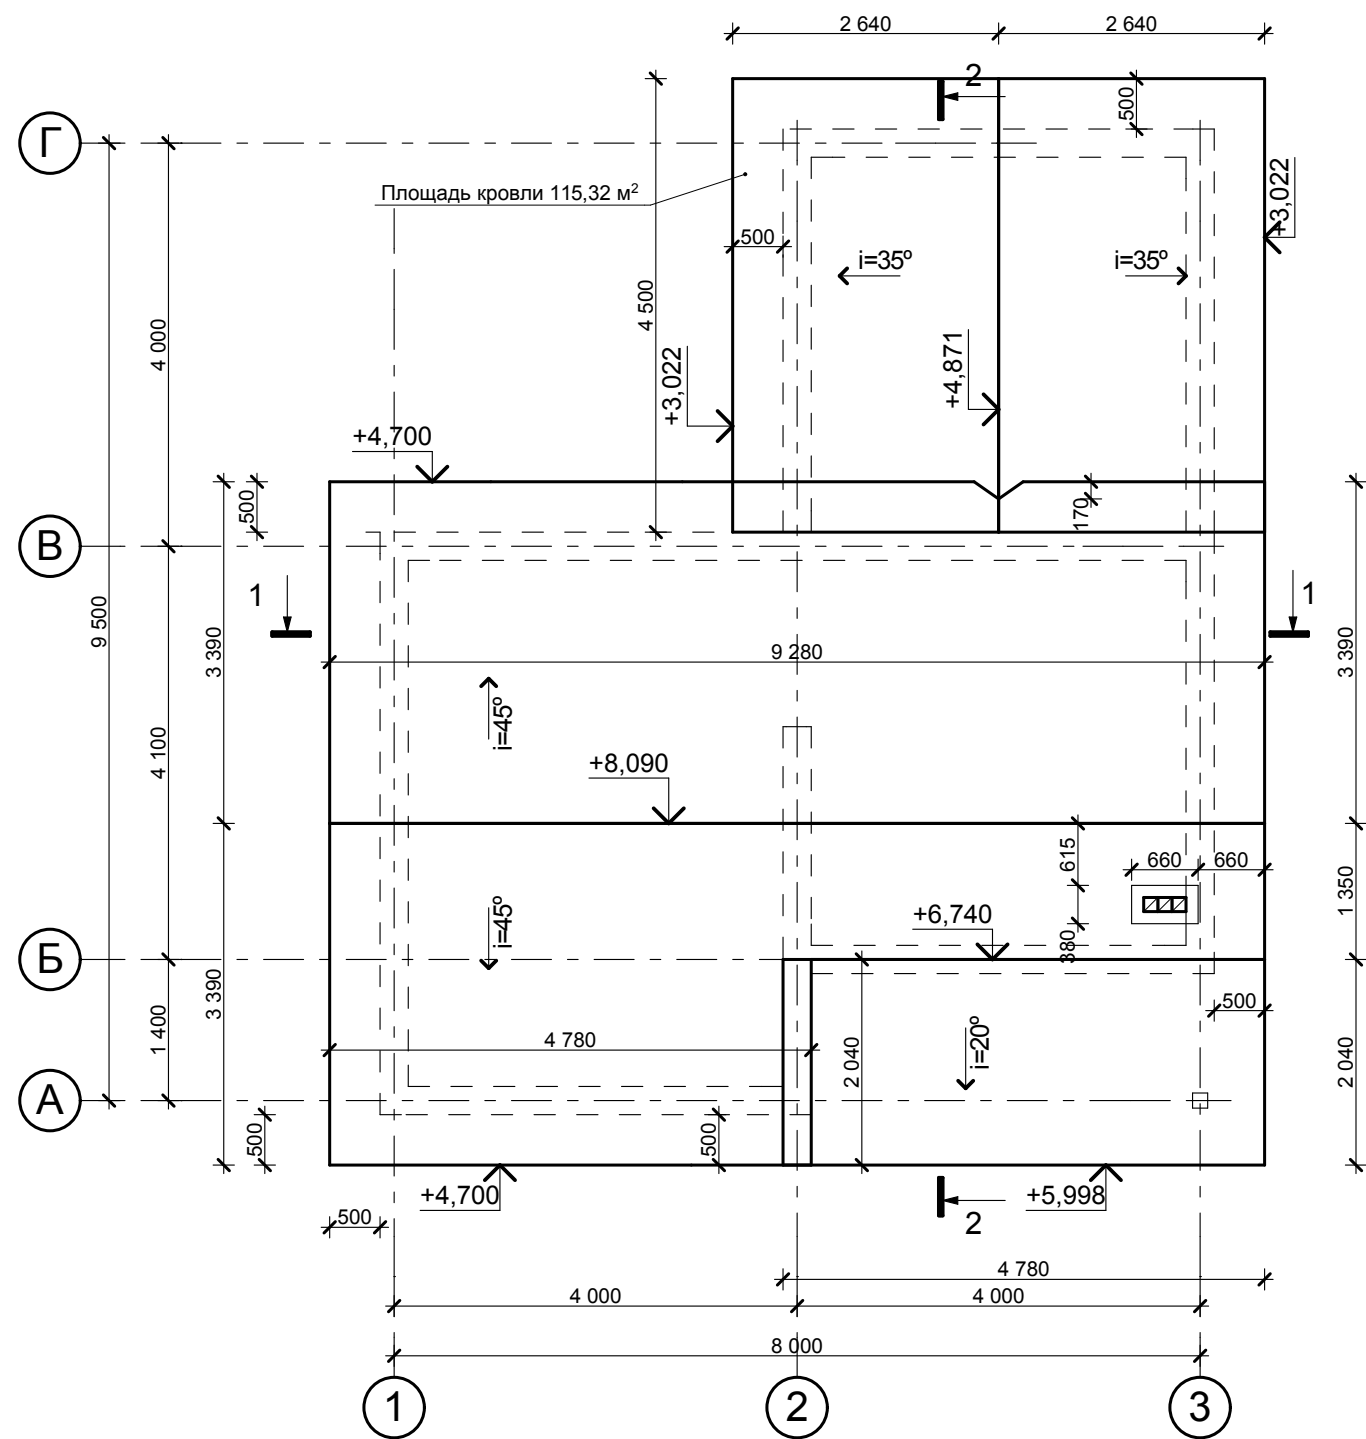

План кровли	Стадия	Лист	Листов
	ЭП	12	13

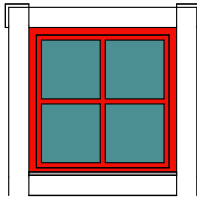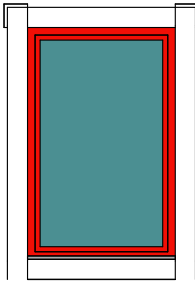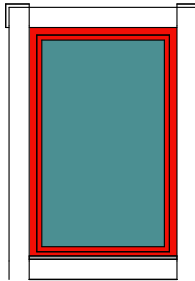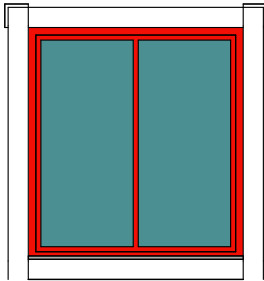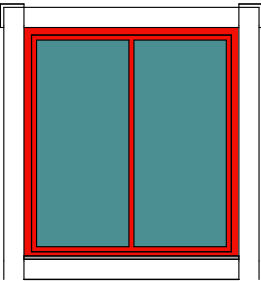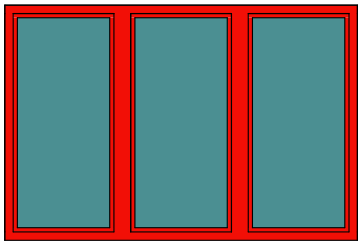Смета окон						
3D-фронтальн...						
Размер Ш x В	900x900	900x1 400	900x1 400	1 300x1 400	1 300x1 400	2 100x1 400
Ориентация	Л	Л	П	Л	П	Л
Количество	2	2	1	2	1	1

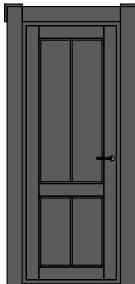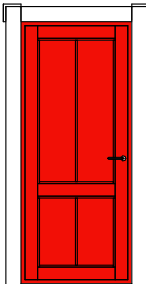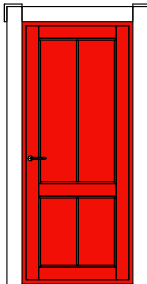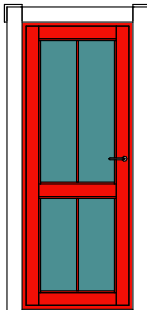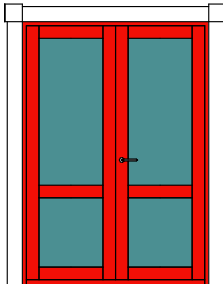Смета дверей					
3D-фронтальн...					
Размер Ш x В	800x2 100	900x2 100	900x2 100	900x2 300	1 500x2 100
Ориентация	Л	Л	П	Л	П
Количество	3	2	1	1	1